



FILE C:\P\INDIA\DESIGN\CR\N\TDIC\II\013
PAGE 01 TO 04
PAGES 51-53 & 94-95
CAL: (R.L. WAGHMANE) (K.S. SURHITA)
CH: (R. L. WAGHMANE) (K.S. SURHITA)
DRG: (P.K. BSE) (K.S. SURHITA)
CH: (R. L. WAGHMANE) (K.S. SURHITA)
TRC: (P.K. BSE) (K.S. SURHITA)
CH: (R. L. WAGHMANE) (K.S. SURHITA)
APPD: (P.K. BSE) (K.S. SURHITA)
CH: (R. L. WAGHMANE) (K.S. SURHITA)
CONT: (K.S. SURHITA) DDG/T-
PUPADHAY

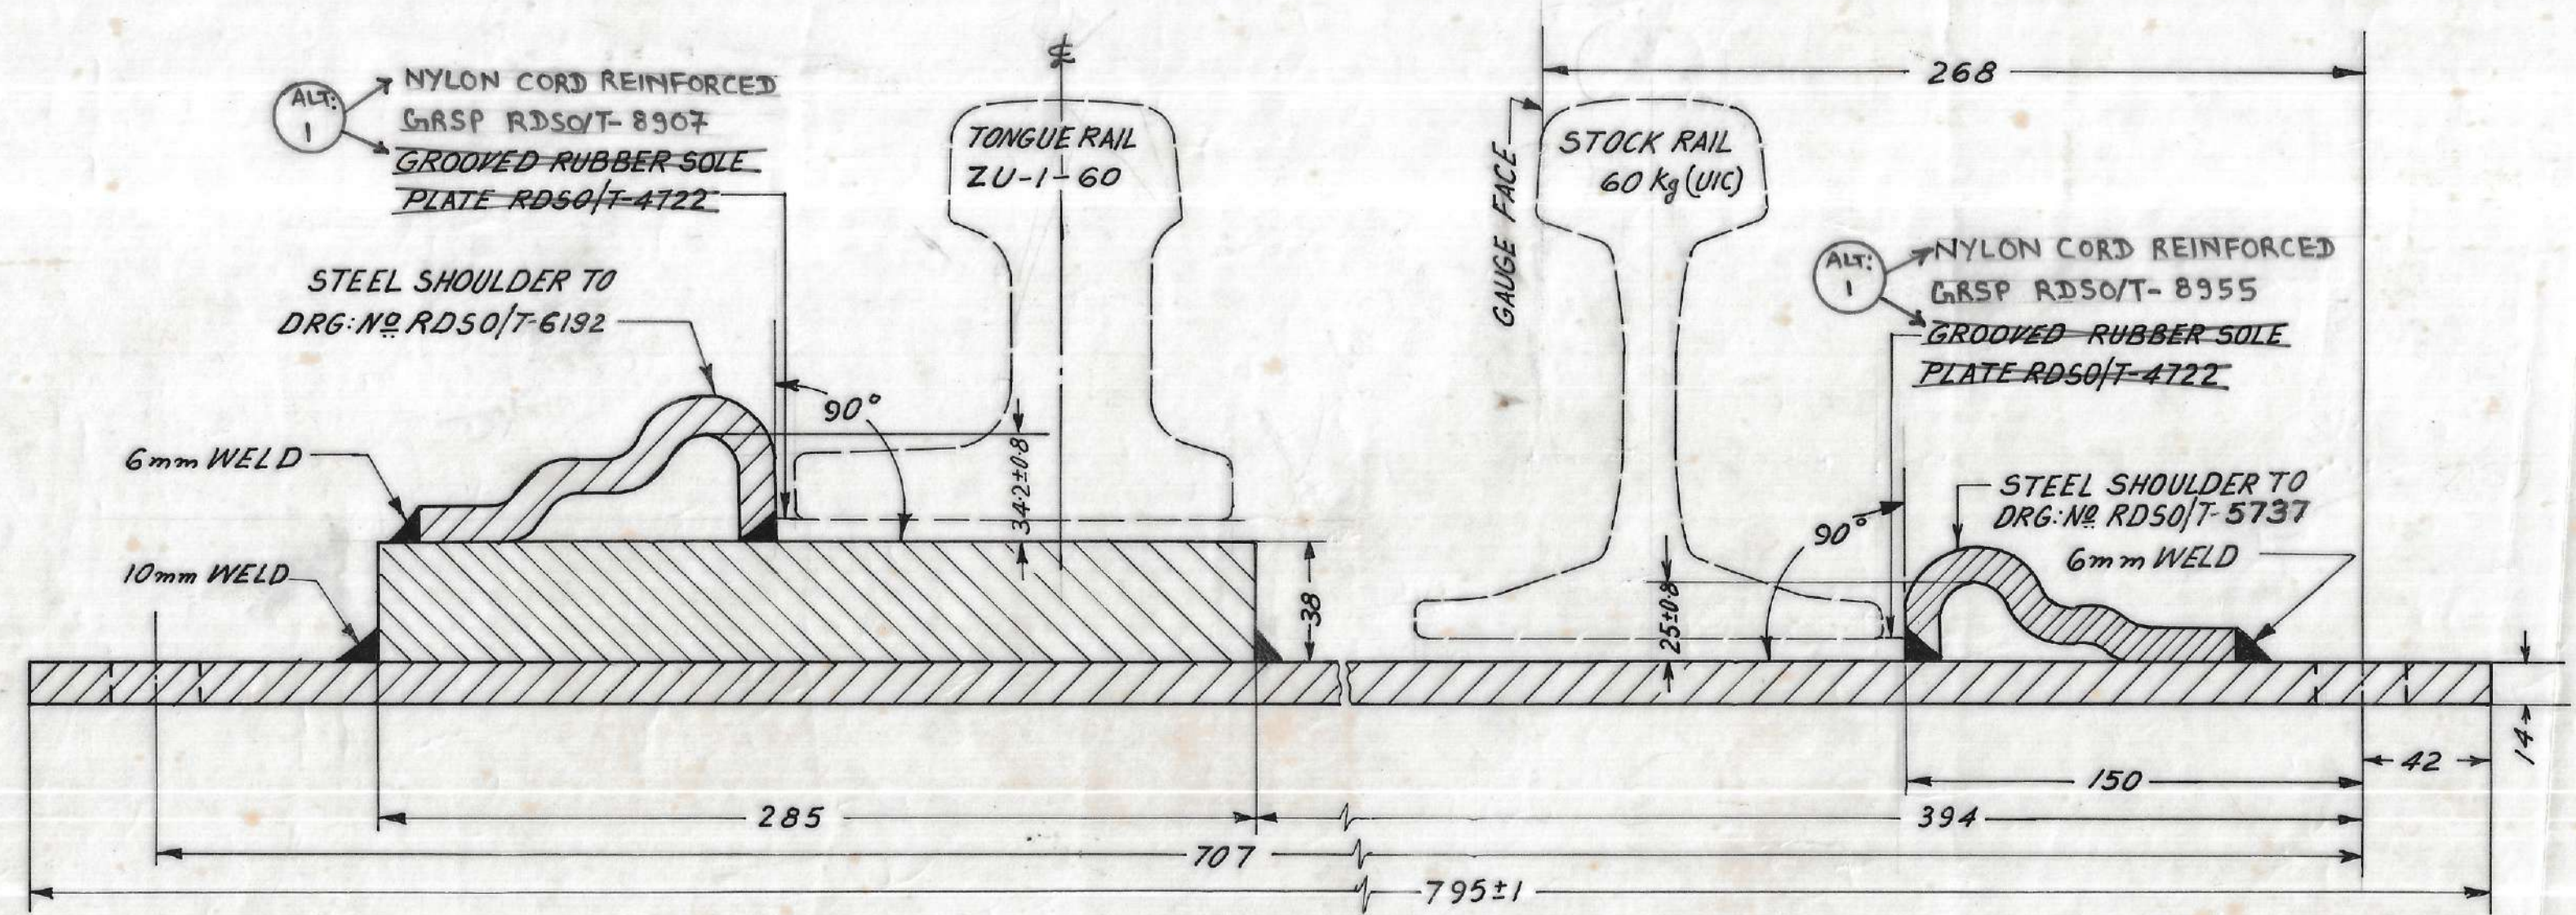

SECTIONAL ELEVATION ON A. B.

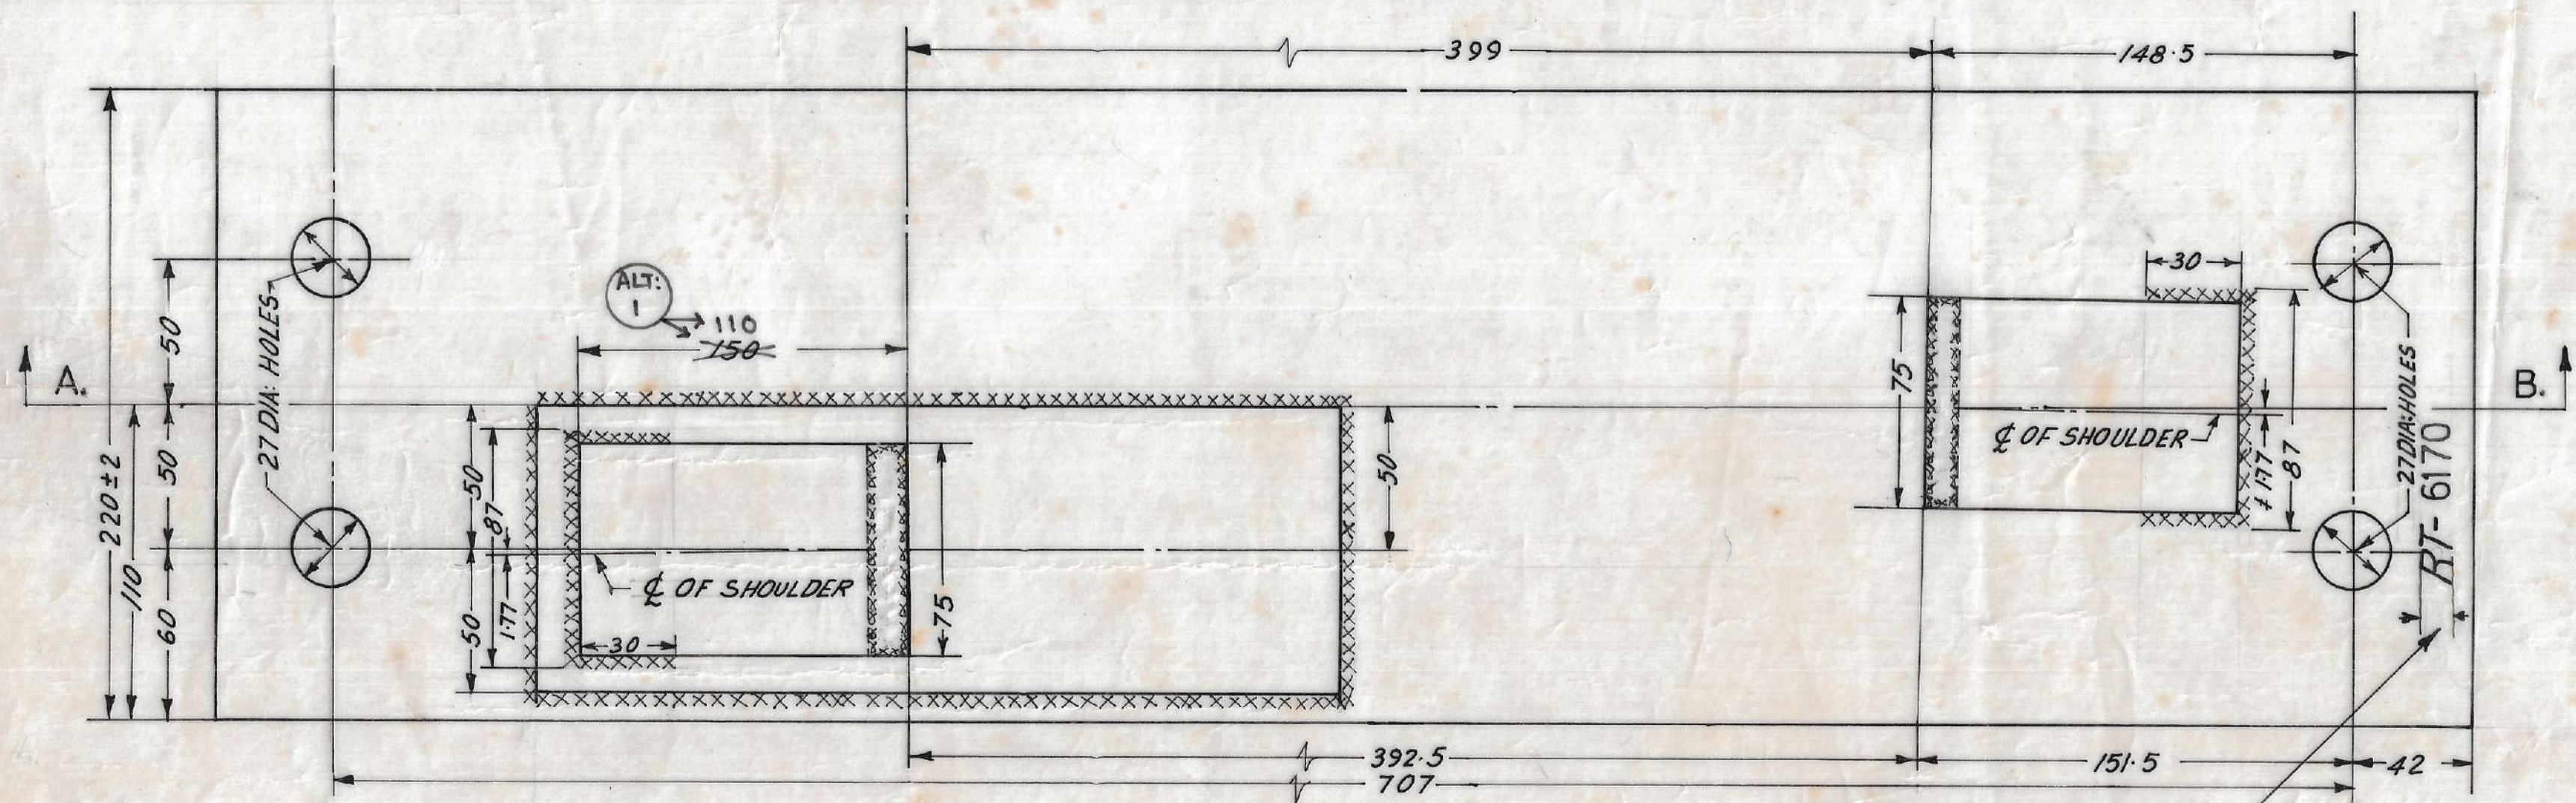


PLAN
(AT SLEEPER NUMBER 24)

4. DIMENSIONS GIVEN SHOW WHERE THE CENTRE AND CROSS-LINES MEET THE EDGES OF THE BEARING PLATE.
3. A TOLERANCE OF 0.8 mm EACH WAY IS PERMITTED IN THE POSITION OF HOLES.
2. LATEST ALTERATION NUMBER SHALL BE CHECKED BEFORE PLACING ORDER.
1. ALL DIMENSIONS ARE IN MILLIMETRES.

NOTE

3. I.R.S. T 10
2. I.S. 2062-1999
1. I.R.S. WELDED BRIDGE
CODE FOR WELDING.

MILLIMETRES

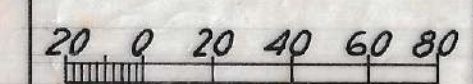

1. DIMENSION IN PLAN
ALTERED
GROOVED RUBBER
SOLE PLATES REPLACED
WITH NYLON CORD
REINFORCED GRSP

ALT: DESCRIPTION DATE

1 EACH	10125 mm CURVED SWITCH WITH ZU-1-60 THICK-WEB TONGUE RAIL FOR 1 IN 12 TURNOUT B.G.(1673mm) FOR 60kg (UIC) ON P.S.C. SLEEPERS.	RDSO/T-6155
NO	DESCRIPTION	NO
OFF	FOR DRAWING	
THIS DRAWING IS THE PROPERTY OF RESEARCH DESIGNS AND STANDARDS ORGANISATION (MINISTRY OF RAILWAYS) LUCKNOW-226011, INDIA AND SHALL NOT BE USED, COPIED OR REPRODUCED IN PART OR WHOLE, WITHOUT PRIOR CONSENT IN WRITING.		
R. D. S. O.		
SPECIAL FLAT BEARING PLATE FOR 10125mm CURVED SWITCH WITH ZU-1-60 THICK-WEB TONGUE RAILS B.G.(1673mm) FOR 60kg (UIC) ON P.S.C. SLEEPER.		
STAMP CANG REVER	ADVANCE 28-11-2002 (T)	RDSO/T-6170