



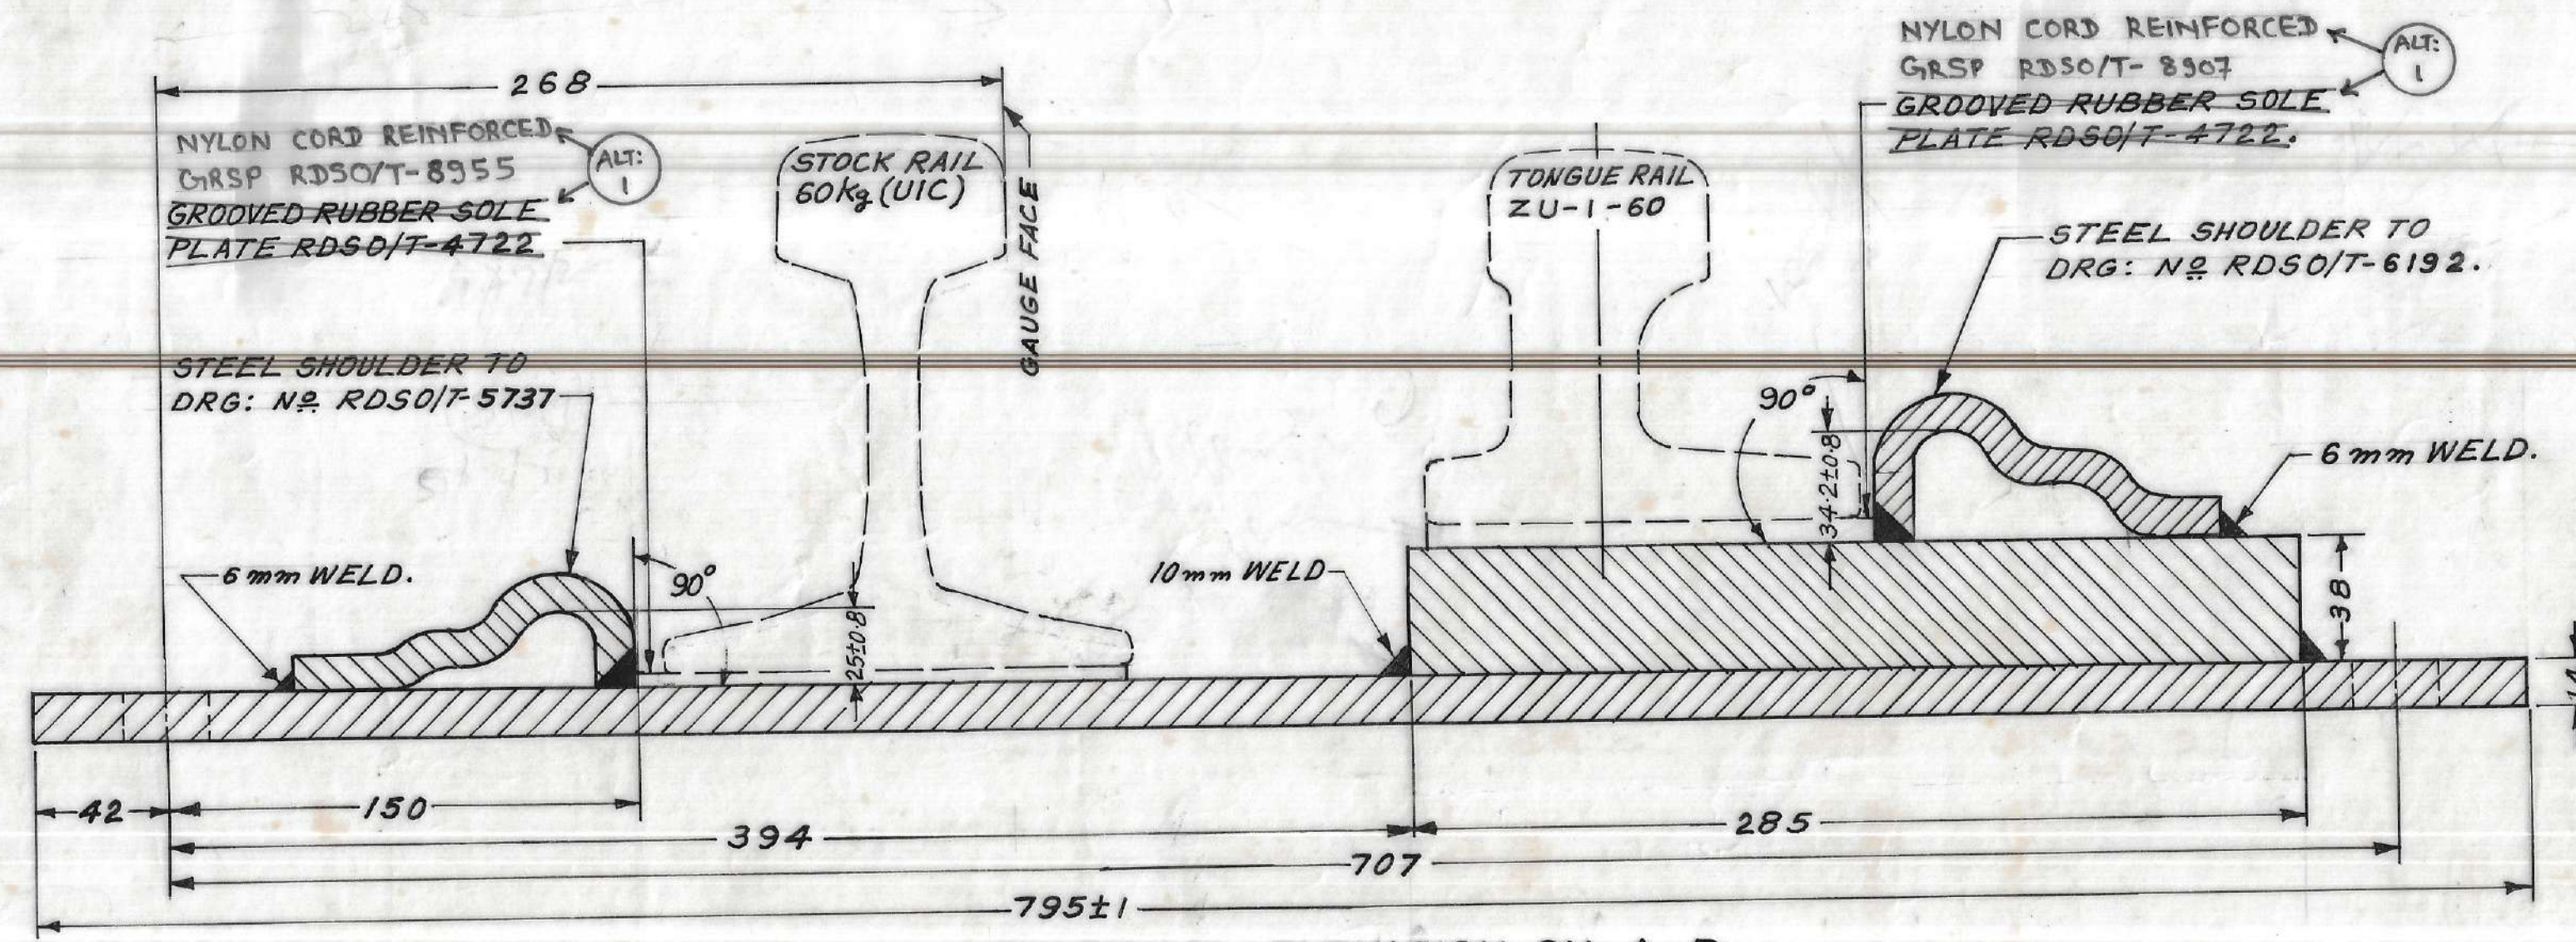

SECTIONAL ELEVATION ON A. B.

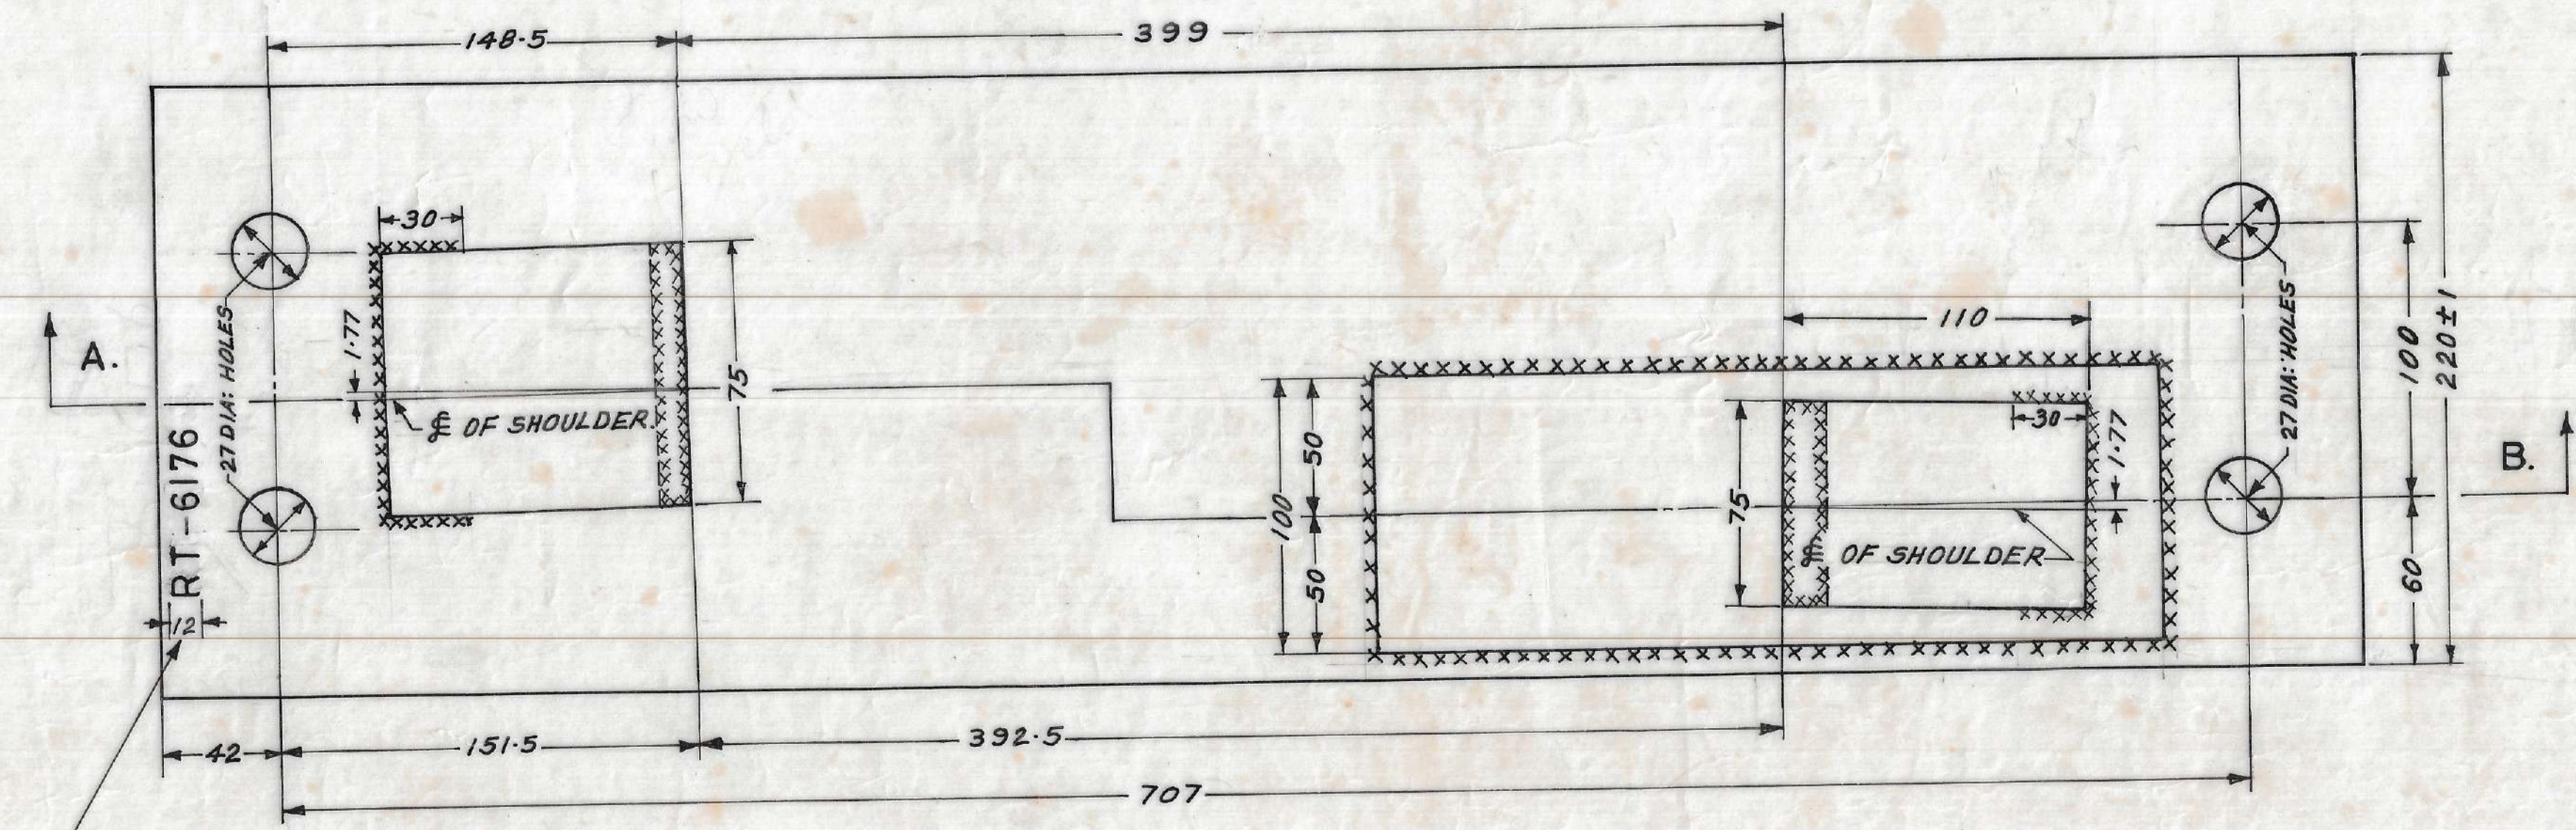


PLAN
(AT SLEEPER NO. 24)

PART NUMBER TO BE STAMPED HERE.

- NOTE
1. ALL DIMENSIONS ARE IN MILLIMETRES.
 2. LATEST ALTERATION NUMBER SHALL BE CHECKED BEFORE PLACING ORDER.
 3. A TOLERANCE OF 0.8 mm EACH WAY IS PERMITTED IN THE POSITION OF HOLES.
 4. DIMENSIONS GIVEN SHOW WHERE THE CENTRE AND CROSS-LINES MEET THE EDGES OF THE BEARING PLATE.

3. I.R.S. T 10.
2. Is: 2062-1999
1. I.R.S. WELDED BRIDGE
CODE FOR WELDING.

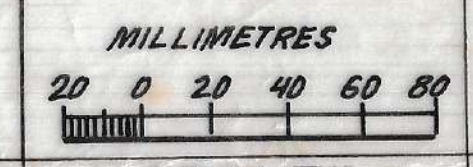

1. GROOVED RUBBER SOLE
PLATES REPLACED WITH
NYLON CORD REINFORCED
GRSP

SPECIFICATION	SCALE	ALT:	DESCRIPTION	DATE
---------------	-------	------	-------------	------

1 EACH	10125mm CURVED SWITCH WITH ZU-1-60 THICK- WEB TONGUE RAIL FOR 1 IN 12 TURNOUT B.G. (1673mm) FOR 60kg (UIC) ON P.S.C. SLEEPERS.	RDSO/T- 6155
Nº OFF	DESCRIPTION FOR DRAWING	Nº
THIS DRAWING IS THE PROPERTY OF RESEARCH DESIGNS AND STANDARDS ORGANISATION (MINISTRY OF RAILWAYS) LUCKNOW-226011, INDIA AND SHALL NOT BE USED, COPIED OR REPRODUCED IN PART OR WHOLE, WITHOUT PRIOR CONSENT IN WRITING.		
R. D. S. O.		
SPECIAL FLAT BEARING PLATE FOR 10125mm CURVED SWITCH WITH ZU-1-60 THICK-WEB TONGUE RAILS BG(1673mm) FOR 60kg (UIC) ON P.S.C. SLEEPER.		
STAMP CHANCE REVISE	ADVANCE (T) 28-11-2002	RDSO/T-6176