
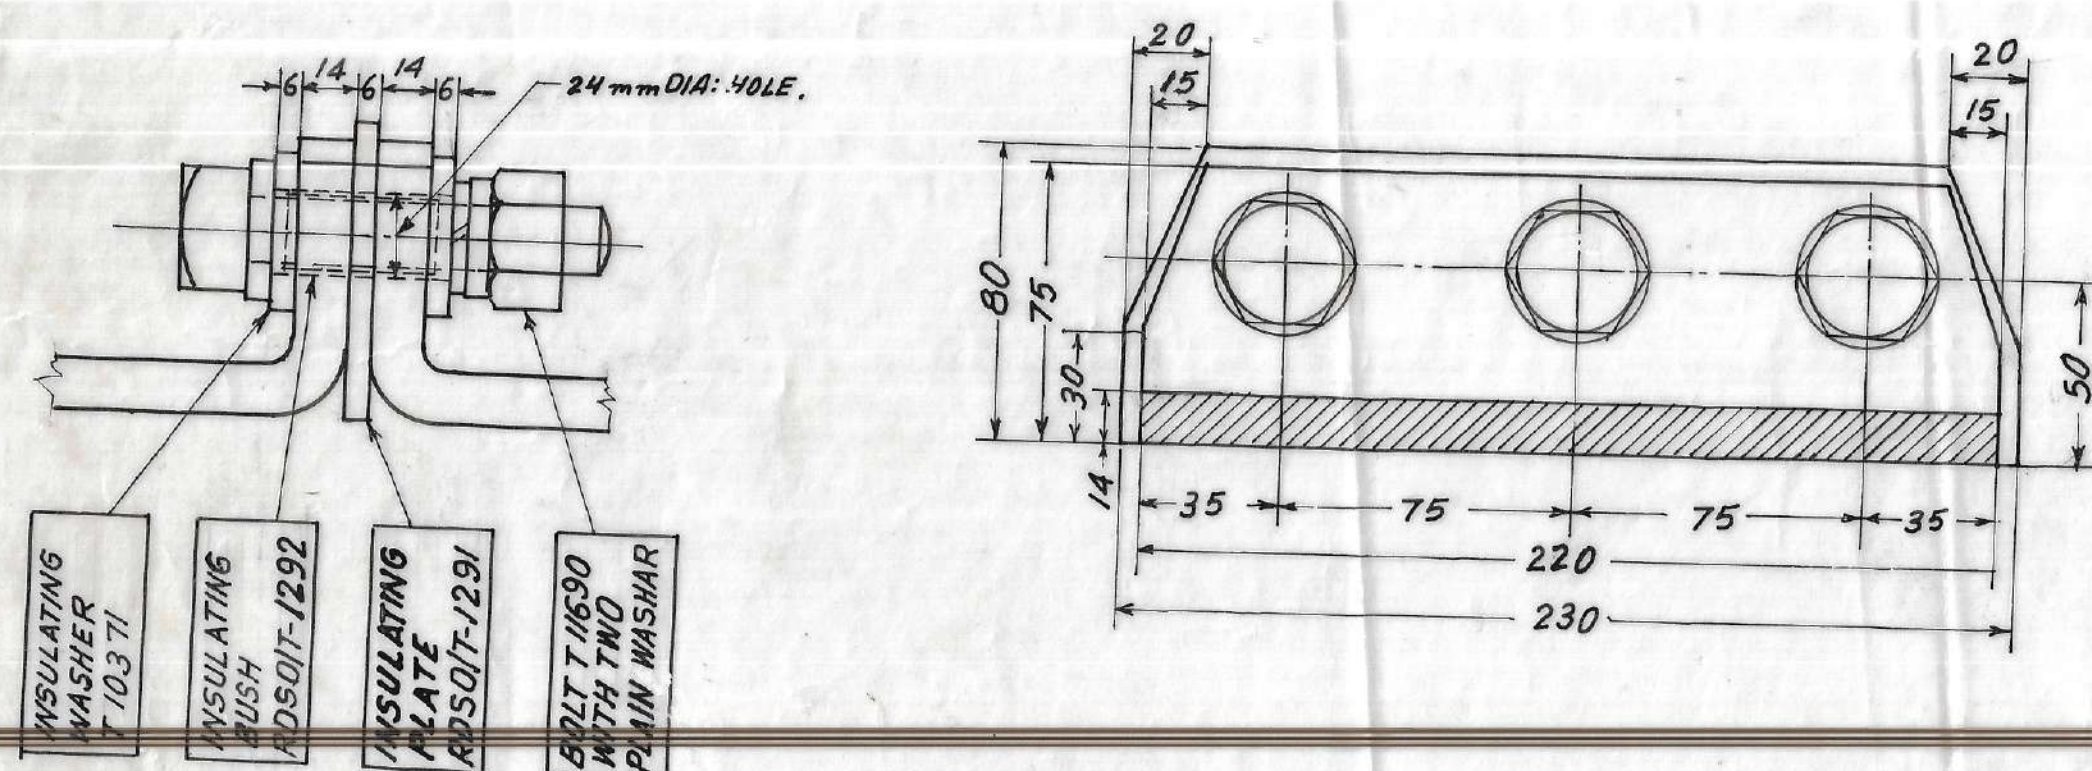
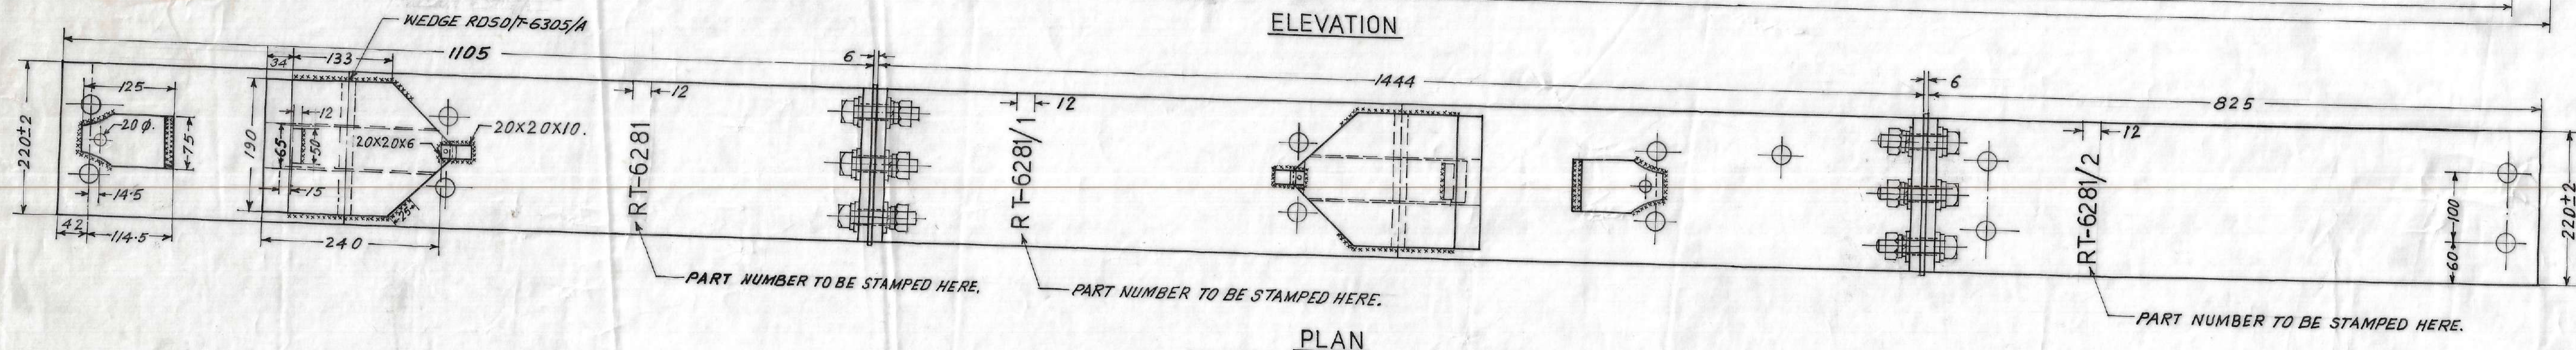


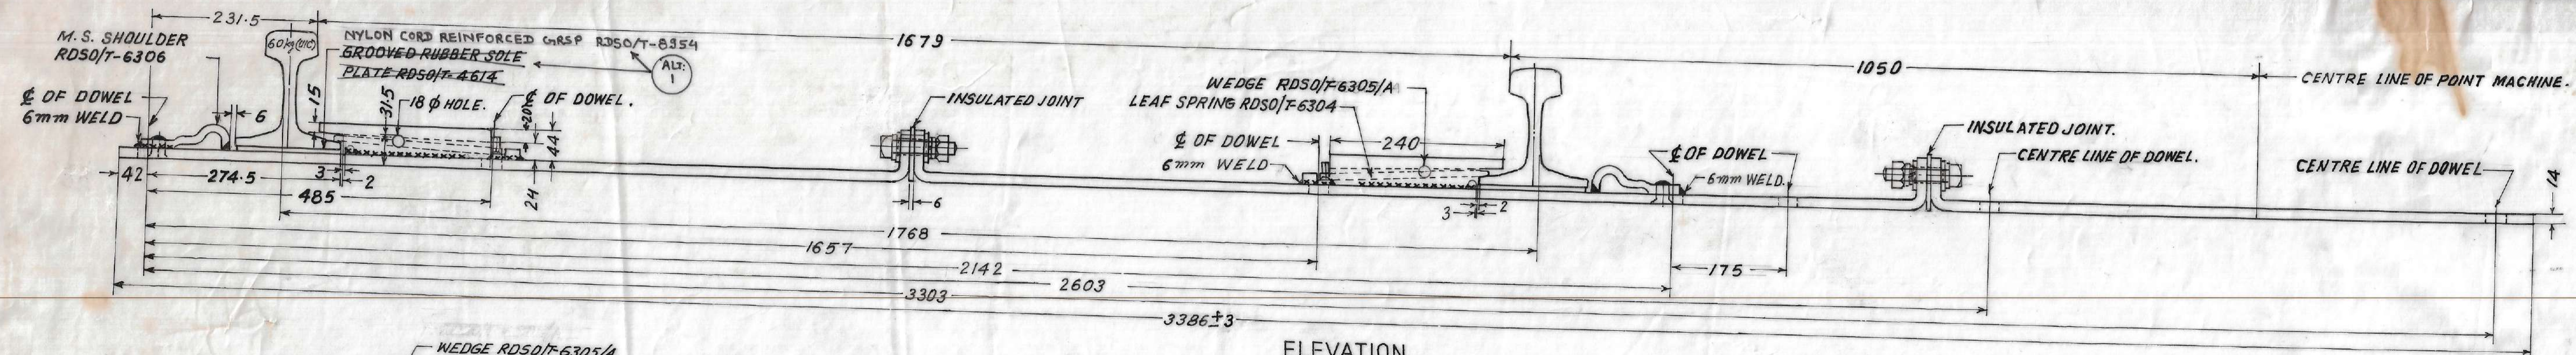

DETAIL OF INSULATED JOINT

10. MIG PROCESS OF WELDING TO BE ADOPTED.
9. SUITABLE HOLES IN THE PLATE FOR SIGNAL FITTINGS & POINT MACHINE MAY BE DRILLED AT SITE.
8. MACHINED SURFACES SHOWN THUS.
7. INSULATING PLATE MAY BE CUT AT ENDS TO SUIT THE FITTINGS.
6. 44mm THICK M.S. PAD SHALL BE WELDED ON THE TIE PLATE.
5. THIS TIE PLATE SHALL BE WELD DOWN ON CONCRETE SLEEPER BY MEANS OF 24mm DIA: PLATE SCREW TO DRG NO. RSJOFT-3912 & SINGLE COIL SPRING WASHER TO DRG NO. T10773.
4. A TOLERANCE OF 0.8mm EACH WAY IS PERMITTED IN THE POSITION OF THE HOLES.
3. ALL HOLES ARE 27mm DIA: EXCEPT WHERE OTHERWISE SHOWN.
2. LATEST ALTERATION NUMBER SHALL BE CHECKED BEFORE PLACING ORDER.
1. ALL DIMENSIONS ARE IN MILLIMETRES.

NOTE

IRS T 10
IS 2062-1999 Gr. B.

	SPECIFICATION
--	---------------

1.	GROOVED RUBBER SOLE PLATES REPLACED WITH NYLON CORD REINFORCED GRSP
----	---

ALT:	DESCRIPTION
------	-------------

20-09-21
DATE

R.	D.	S.	O.
EXTENDED TIE PLATE(INSULATED) FOR 6400mm CURVED SWITCH WITH ZU-I-60 THICK-WEB TONGUE RAILS B.G.(1673mm) FOR 60kg (UIC) ON PSC SLEEPERS.			
STANLEY PSC REV. P		ADVANCE 24.02.04.	(T)
RDSO/T-6281 TO		RDSO/T-6281/2	