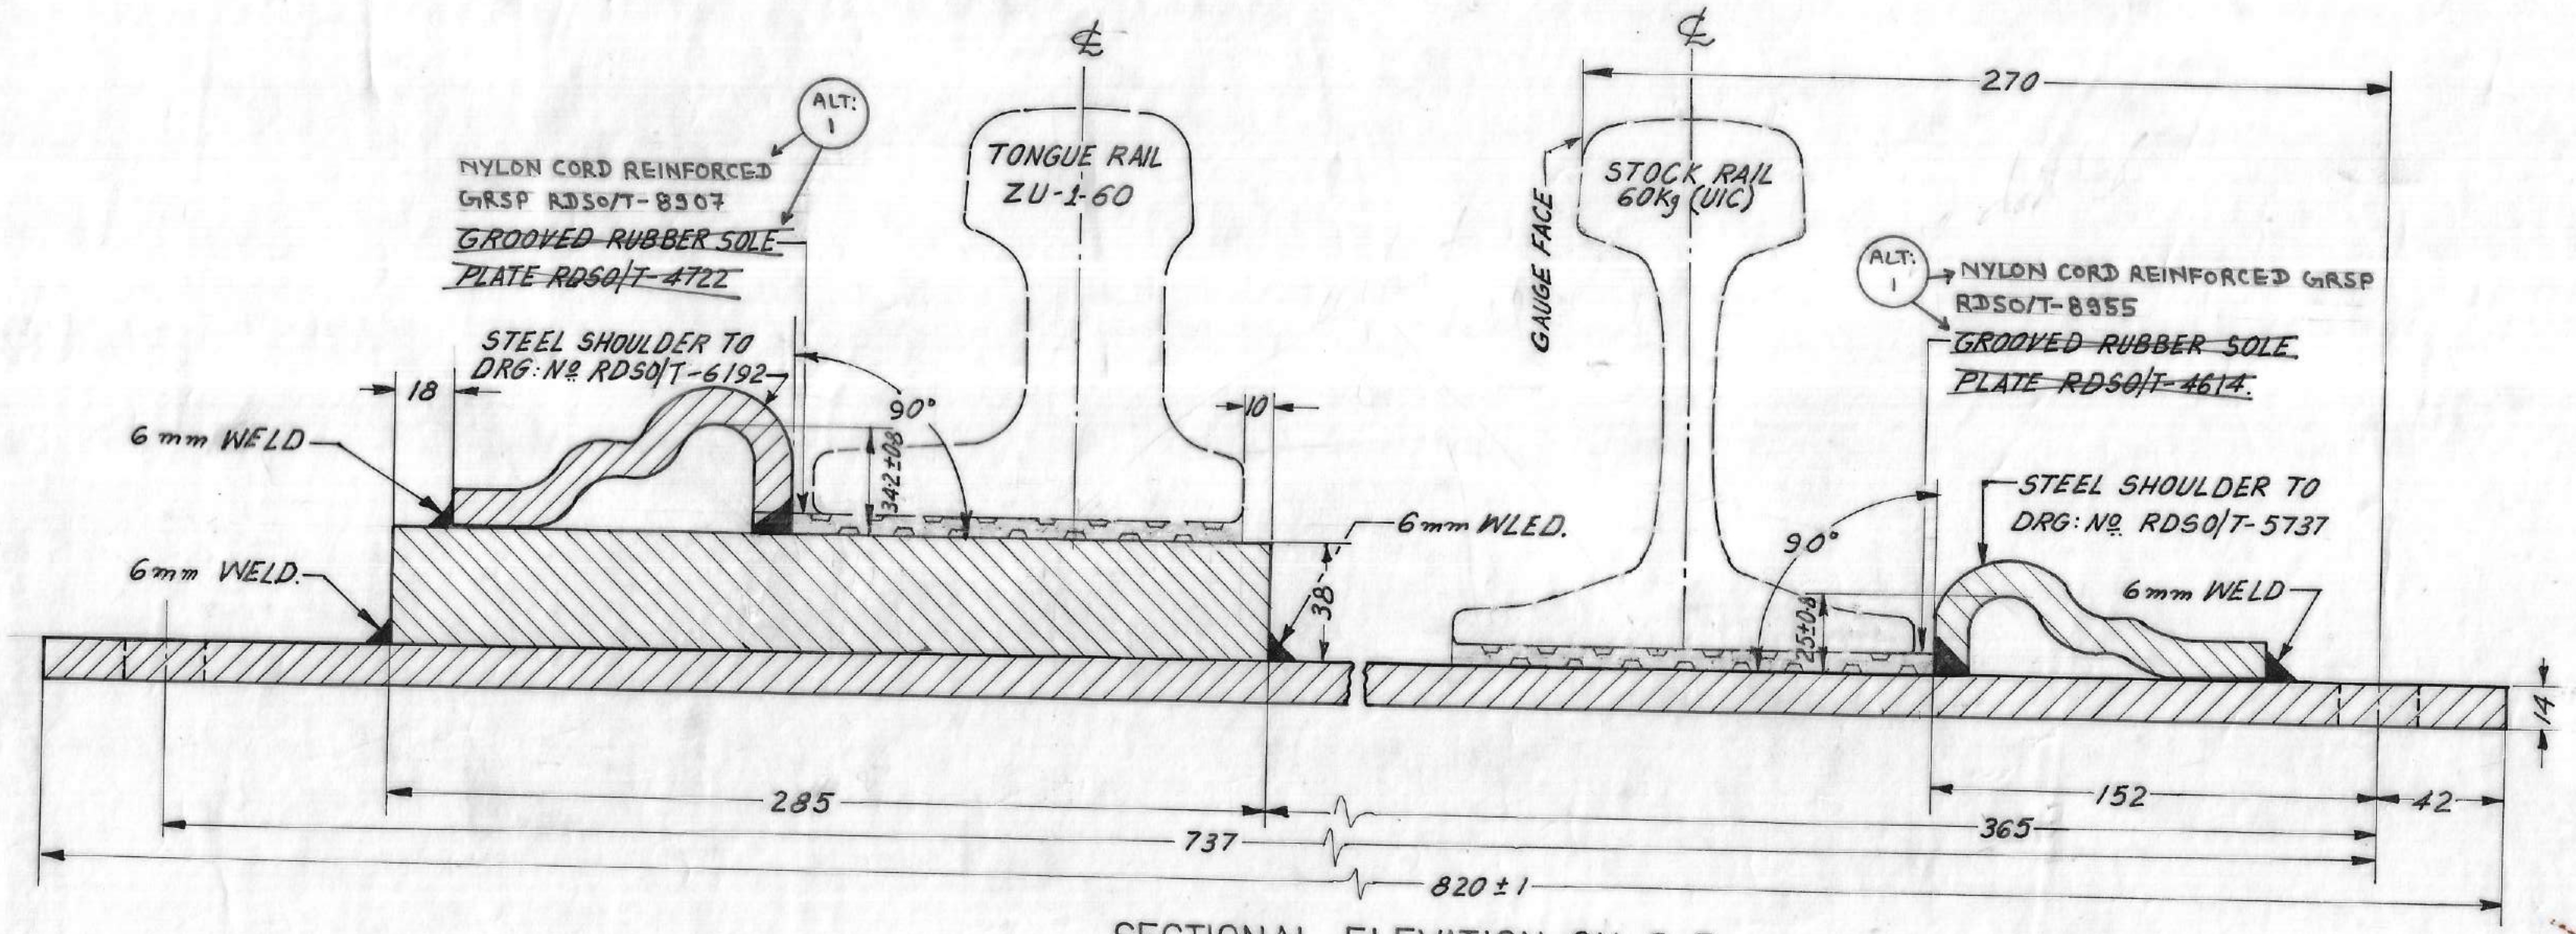

SECTIONAL ELEVATION ON C. D.

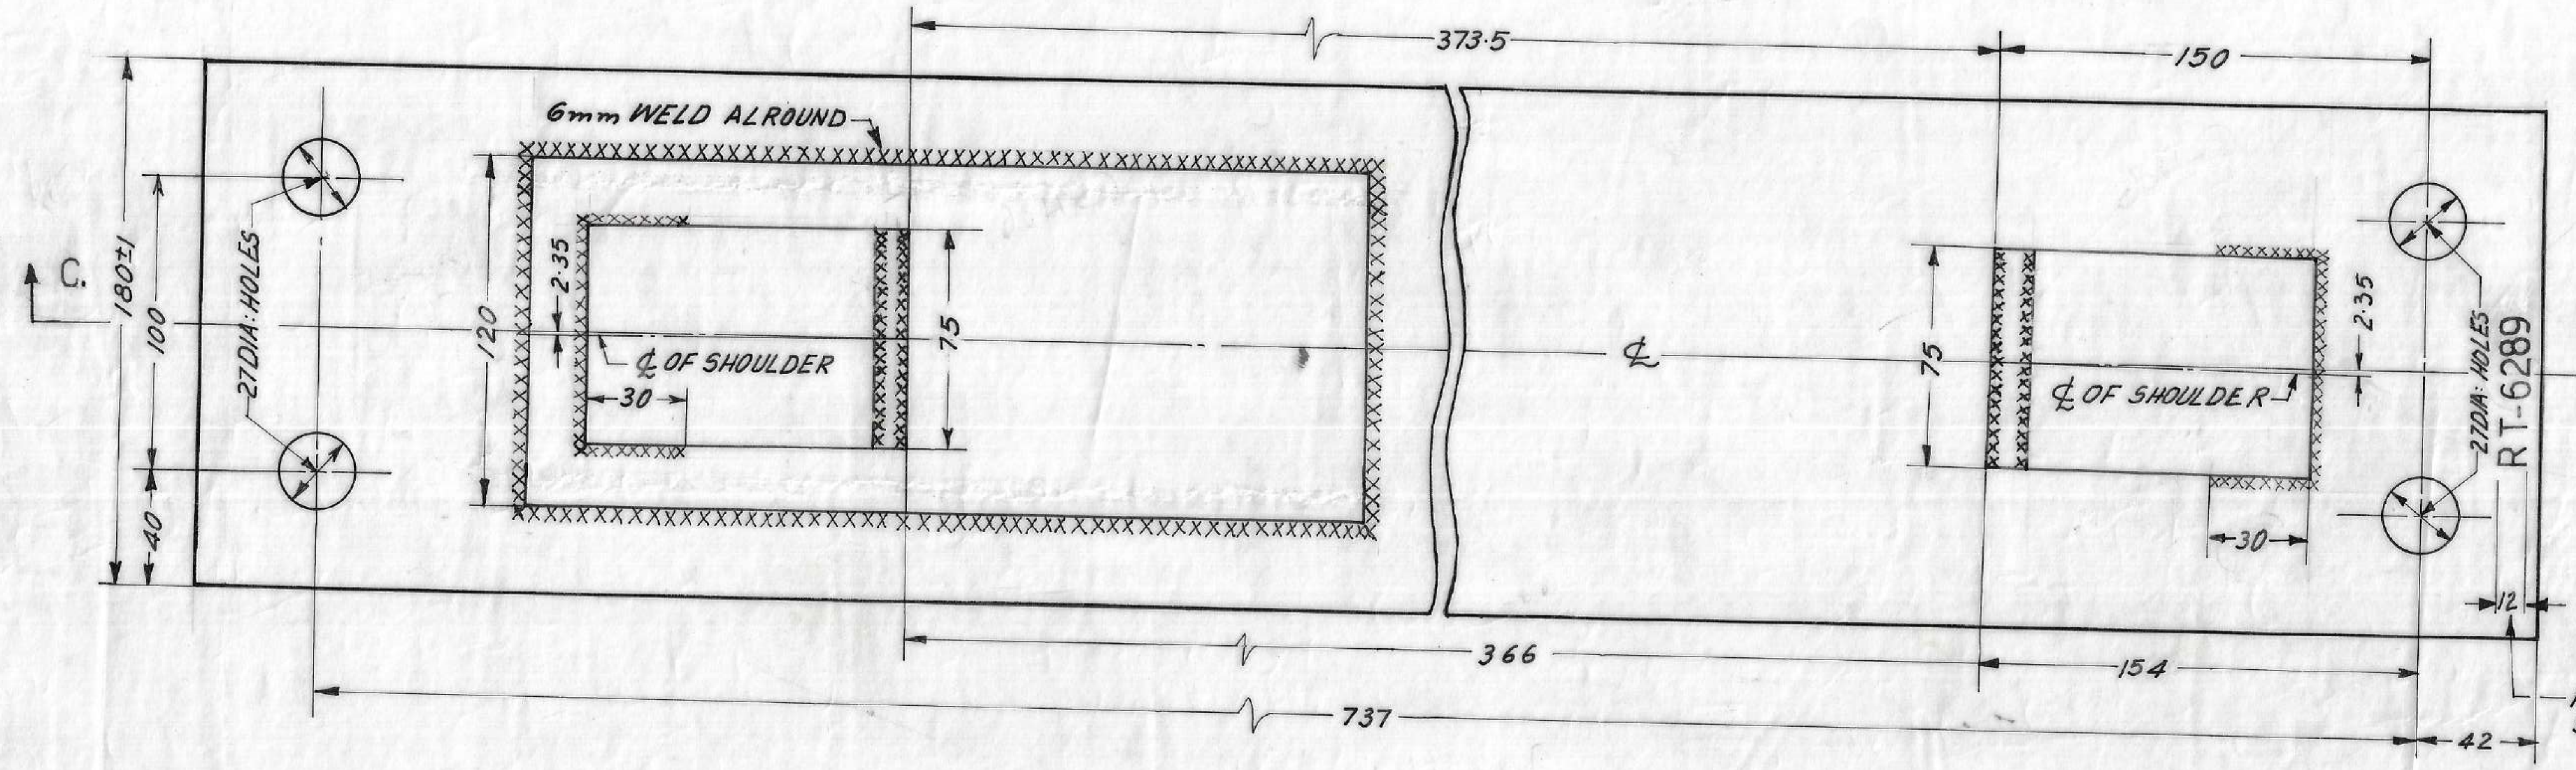

PLAN

5. MIG PROCESS OF WELDING TO BE ADOPTED.
4. DIMENSIONS GIVEN SHOW WHERE THE CENTRE AND CROSS-LINES MEET THE EDGES OF THE BEARING PLATE.
3. A TOLERACE OF 0·8mm EACH WAY IS PERMITTED IN THE POSITION OF HOLES.
2. LATEST ALTERATION NUMBER SHALL BE CHECKED BEFORE PLACING ORDER.
1. ALL DIMENSIONS ARE IN MILLIMETRES.

NOTE

3. IRS. T-10.
2. IS: 2062-1999. Gr.-'B'
1. IRS. WELDED BRIDGE CODE FOR WELDING.

SPECIFICATION

MILLIMETRES
20 0 20 40 60 80

SCALE

ALT:	DESCRIPTION	DATE
1.	GROOVED RUBBER SOLE PLATES REPLACED WITH NYLON CORD REINFORCED GRSP	20-09-21

Nº OFF	DESCRIPTION	Nº
1 EACH	6400 mm CURVED SWITCH WITH ZU-1-60 THICK-WEB TONGUE RAIL FOR 1 IN 8·5 TURNOUT B.G.(1673mm) FOR 60Kg(UIC) ON P.S.C. SLEEPERS.	RDSO/T-6280
	FOR DRAWING	

THIS DRAWING IS THE PROPERTY OF
RESEARCH DESIGNS AND STANDARDS ORGANISATION
(MINISTRY OF RAILWAYS)
LUCKNOW-226011, INDIA
AND SHALL NOT BE USED, COPIED OR REPRODUCED IN PART OR WHOLE, WITHOUT PRIOR CONSENT IN WRITING.

R. D. S. O.

SPECIAL FLAT BEARING PLATE FOR 6400mm CURVED SWITCH WITH ZU-1-60 THICK-WEB TONGUE RAILS B.G.(1673mm) FOR 60Kg (UIC) ON P.S.C. SLEEPERS.

STANDD. ----------
CANCLD. ----------
REVD. ----------
ADVANCE
24.02.04
(T)

RDSO/T-6289

FILE CT/PTX/TWS	CR. No. 7DIC/II/03/22	CAL:	CAL:	DRG:	DRG:	TRC:	TRC:	SE/D	DDS/T-II
DESIGN PAGE 19T021	PAGES 33 TO 37	BY. R.L.WAGHMARE	CH: V.R.SARSWAT	BY. P.K.BOSE	CH: M.N.U.FARIDI	BY. M.N.U.FARIDI	CH: P.K.BOSE	R.L.WAGHMARE	P.UPADHYAY