



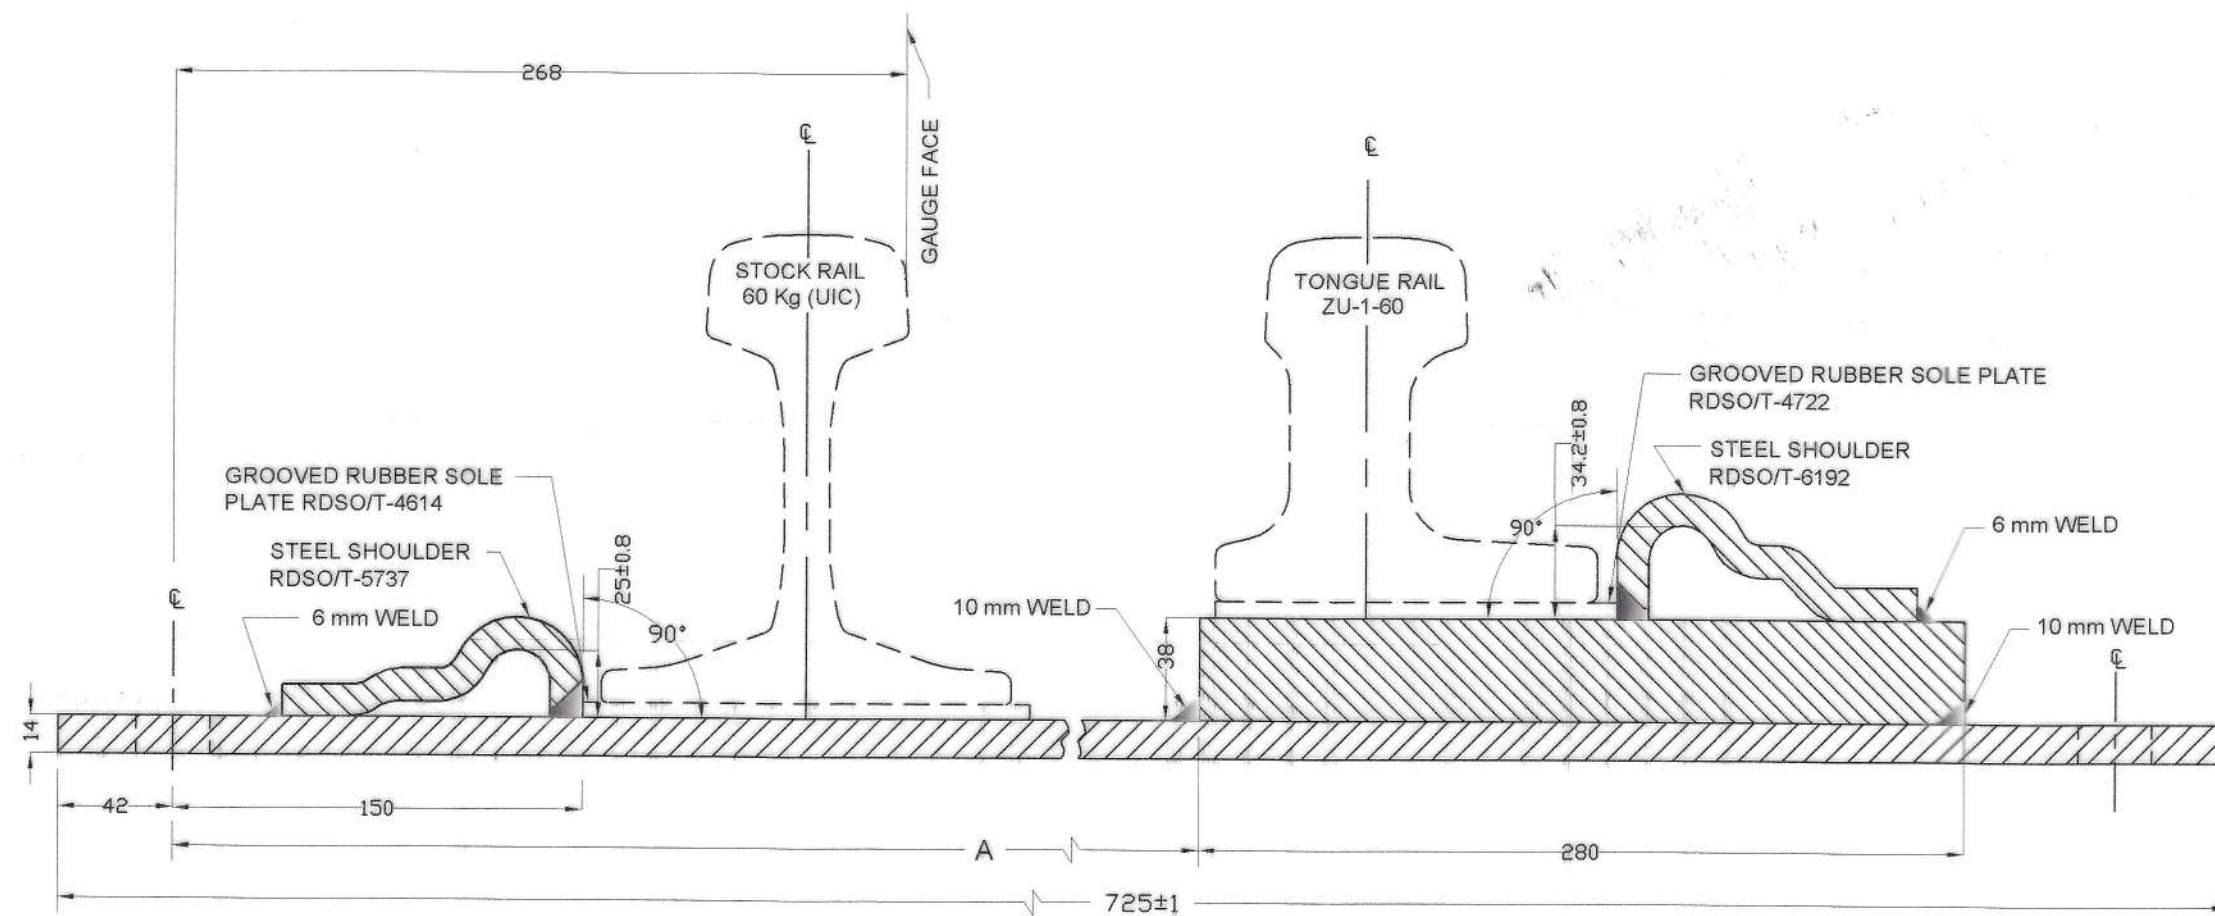

SECTIONAL ELEVATION ON 'AB'

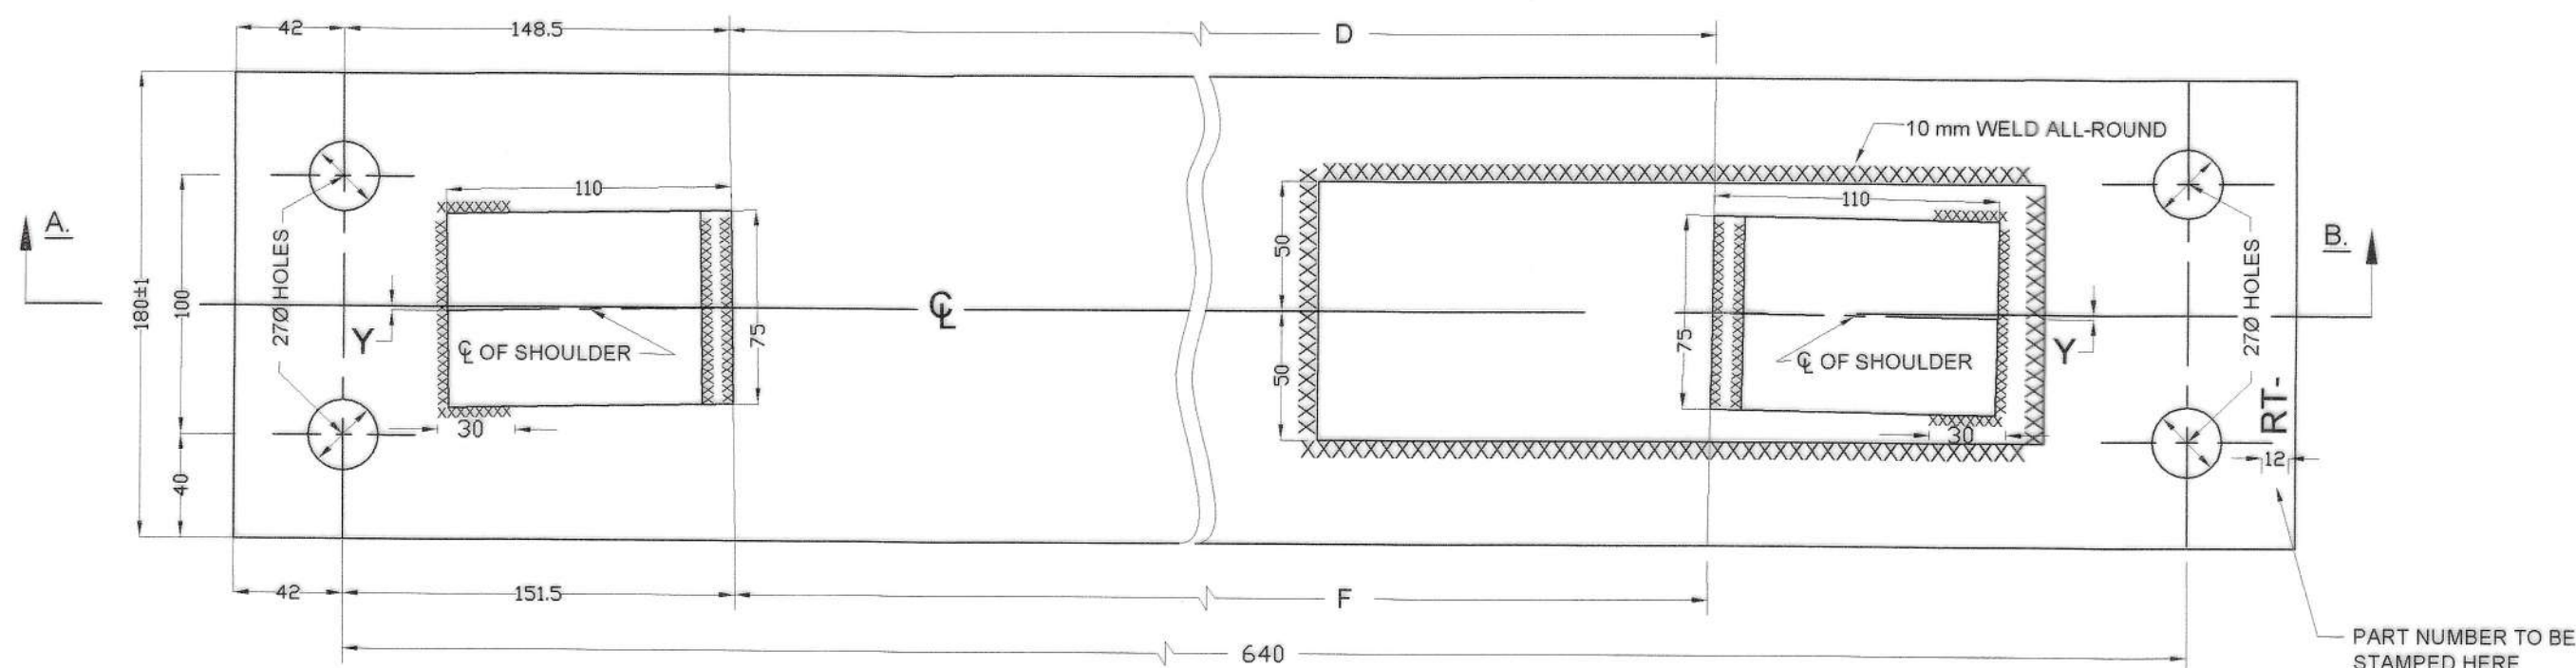

4. DIMENSIONS GIVEN SHOWN WHERE THE CENTRE AND CROSS-LINES MEET THE EDGES OF THE BEARING PLATE.
3. A TOLERANCE OF 0.8 mm EACH WAY IS PERMITTED IN THE POSITION OF HOLES.
2. LATEST ALTERATION NUMBER SHALL BE CHECKED BEFORE PLACING ORDER.
1. ALL DIMENSIONS ARE IN MILLIMETERS.

NOTE

3. IRS. T-10.
2. IS: 2062-1999
1. IRS. WELDED BRIDGE CODE FOR WELDING.

NOT TO SCALE

1.

REVISÉ & REDRAWN

23-09-2021

THIS DRAWING IS THE PROPERTY OF
RESEARCH DESIGNS AND STANDARDS ORGANISATION
(MINISTRY OF RAILWAYS)
LUCKNOW-226011, INDIA
AND SHALL NOT BE USED, COPIED OR REPRODUCED IN
PART OR WHOLE, WITHOUT PRIOR CONSENT IN WRITING

R. D. S. O

SPECIAL FLAT BEARING PLATE FOR
11200 mm CURVED SWITCH WITH
ZU-1-60 THICK-WEB TONGUE RAILS
B.G. (1673 mm) FOR 60 Kg (UIC) ON
P.S.C. SLEEPERS.

STAN _D	ADVANCE	(T
CANC _D	29.01.2010	
REV _D		

RDSO/T-7087 & RDSO/T-7088