



FILE S. No.	CT/PTX/TWS/DESIGN n.p. No. 17 (Sl. No. 877 TO -----)	C.R. No. PAGES	NIL	DRG. BY:	S.K. SAGAR (SSE/Track)	DRG. CH:	RAM MOHAN (SSE/Track)	DD/TP & C	M.K. MANDAL (SSE/Track)	APPD.	A.K. SHARMA	DST - III	RITU RAJ
----------------	--	-------------------	-----	-------------	---------------------------	-------------	--------------------------	-----------	----------------------------	-------	-------------	-----------	----------

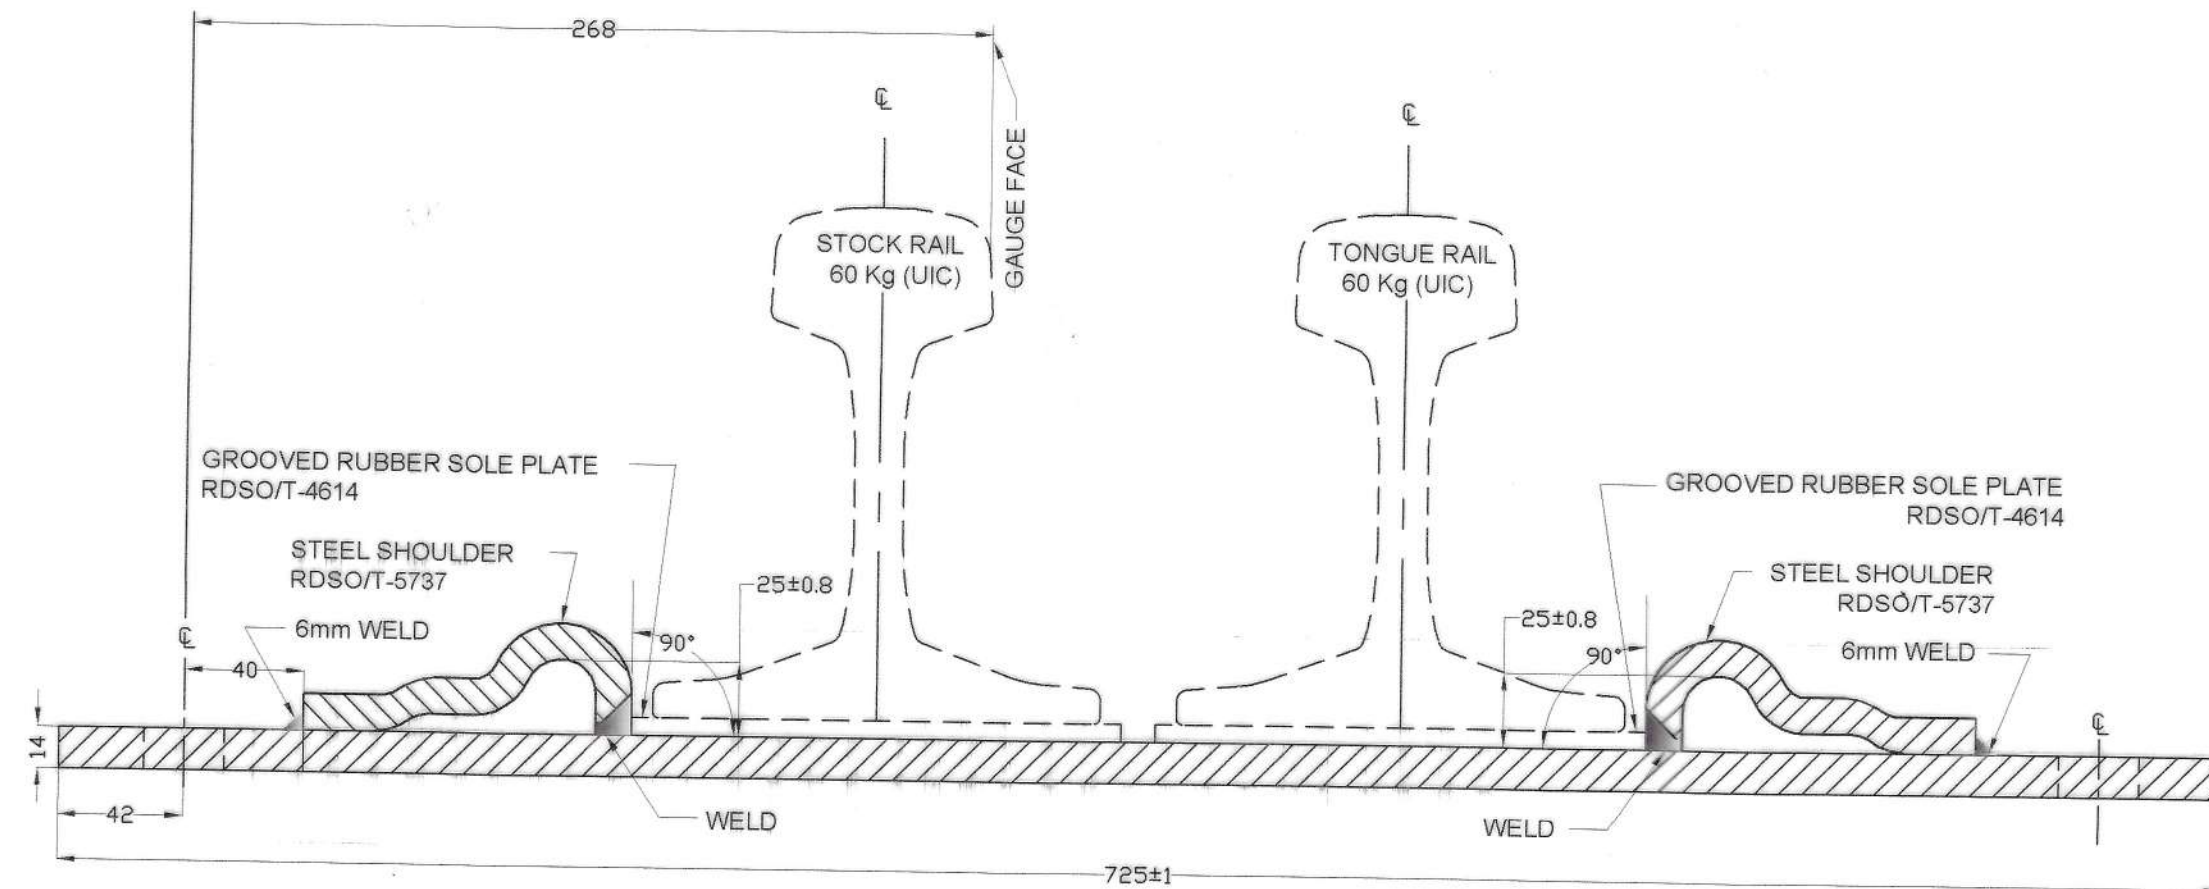

SECTIONAL ELEVATION ON 'AB'

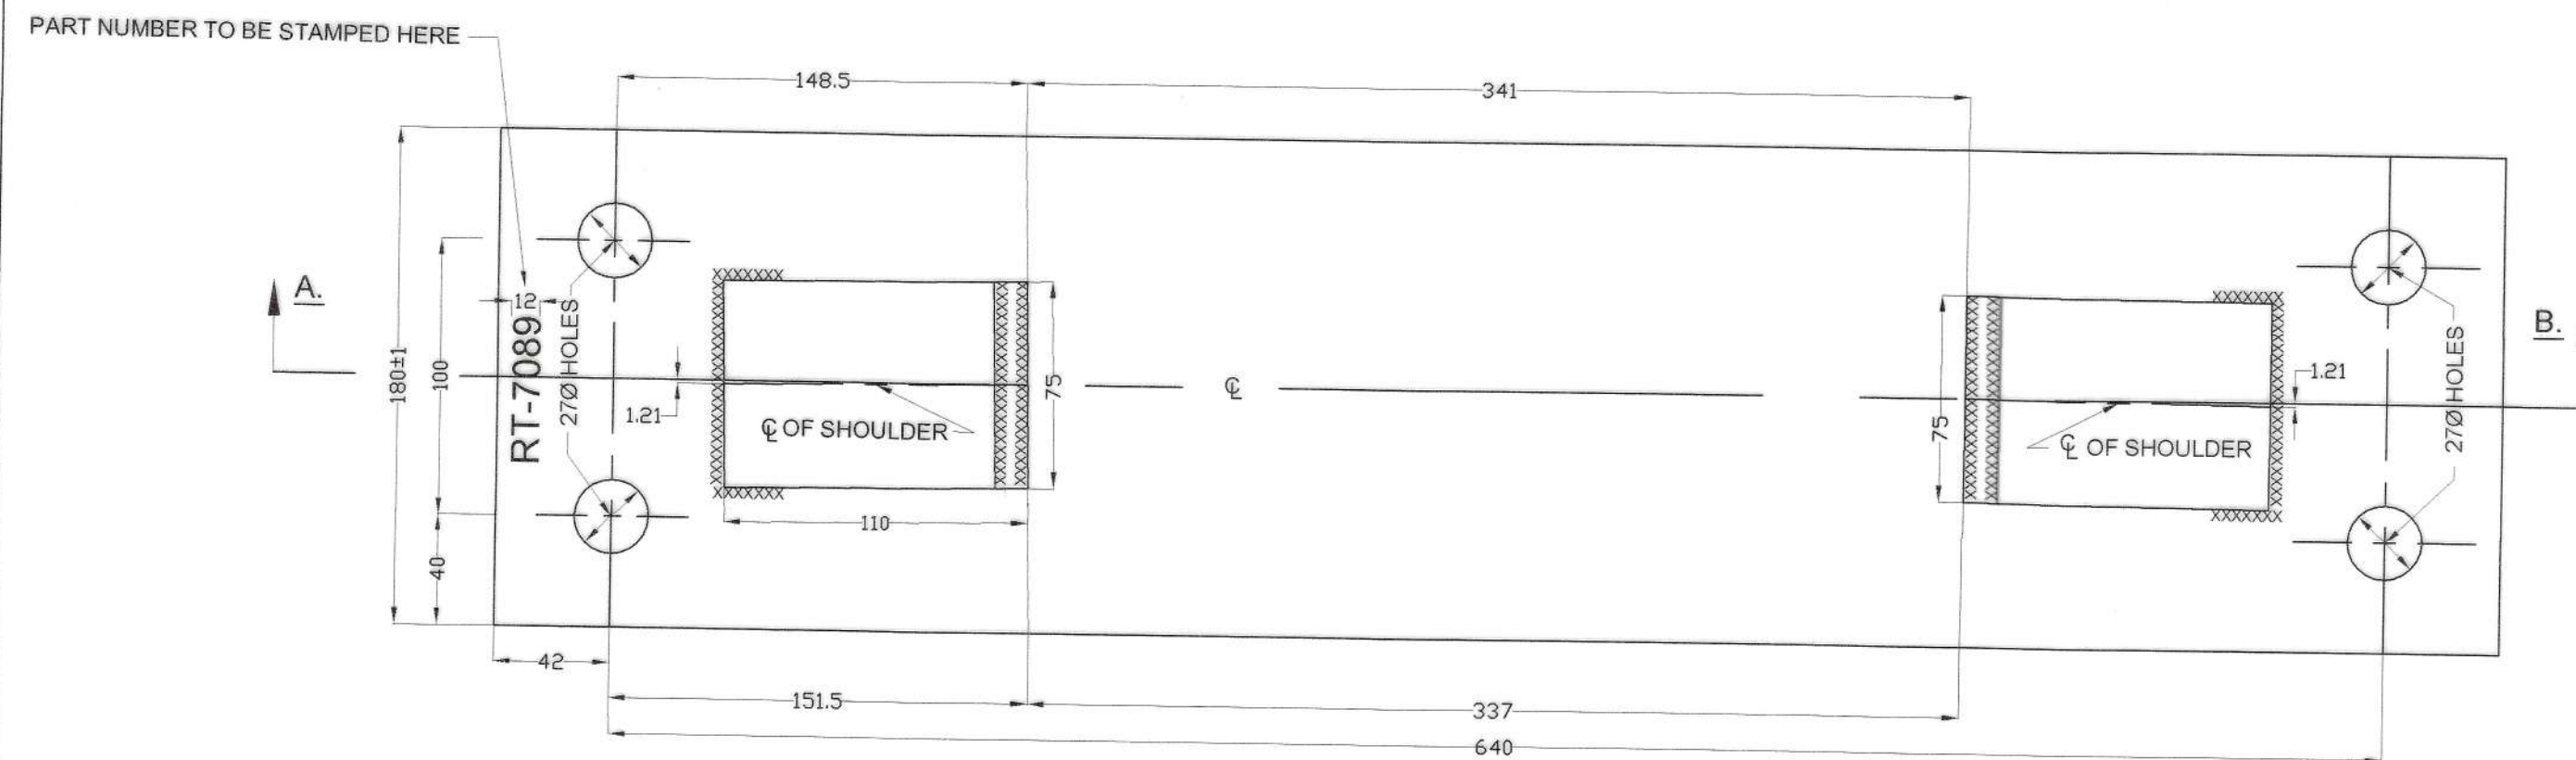

PLAN

3. A TOLERANCE OF 0.8 mm EACH WAY IS PERMITTED IN THE POSITION OF HOLES.
2. LATEST ALTERATION NUMBER SHALL BE CHECKED BEFORE PLACING ORDER.
1. ALL DIMENSIONS ARE IN MILLIMETERS.

NOTE

2. IS: 2062-1992
1. IRS WELDED BRIDGE CODE
FOR WELDING.

SPECIFICATION

NOT TO SCALE

SCALE

01

ALT:

REVISED & REDRAWN

DESCRIPTION

23-09-2021

DATE

THIS DRAWING IS THE PROPERTY OF
RESEARCH DESIGNS AND STANDARDS ORGANISATION
(MINISTRY OF RAILWAYS)
LUCKNOW-226011, INDIA
AND SHALL NOT BE USED, COPIED OR REPRODUCED IN
PART OR WHOLE, WITHOUT PRIOR CONSENT IN WRITING

R. D. S. O.

SPECIAL FLAT BEARING PLATE
FOR 11200 mm CURVED SWITCH
WITH ZU-1-60 THICK-WEB TONGUE
RAILS B.G. (1673 mm) FOR 60 Kg
(UIC) ON P.S.C. SLEEPERS.

STAN:-----
CANC:-----
REV:-----

ADVANCE
29-01-2010

(T)

RDSO/T-7089