



FILE S. No.	CT/PTX/TWS/DESIGN	C.R. No. PAGES	NIL	DRG. BY:	S.K. SAGAR (SSE/Track)	DRG. CH:	RAM MOHAN (SSE/Track)	M.K. MANDAL (SSE/Track)	DD/T/P & C	A.K. SHARMA	APPD:	DST - III	RITU RAJ
-------------	-------------------	----------------	-----	----------	------------------------	----------	-----------------------	-------------------------	------------	-------------	-------	-----------	----------

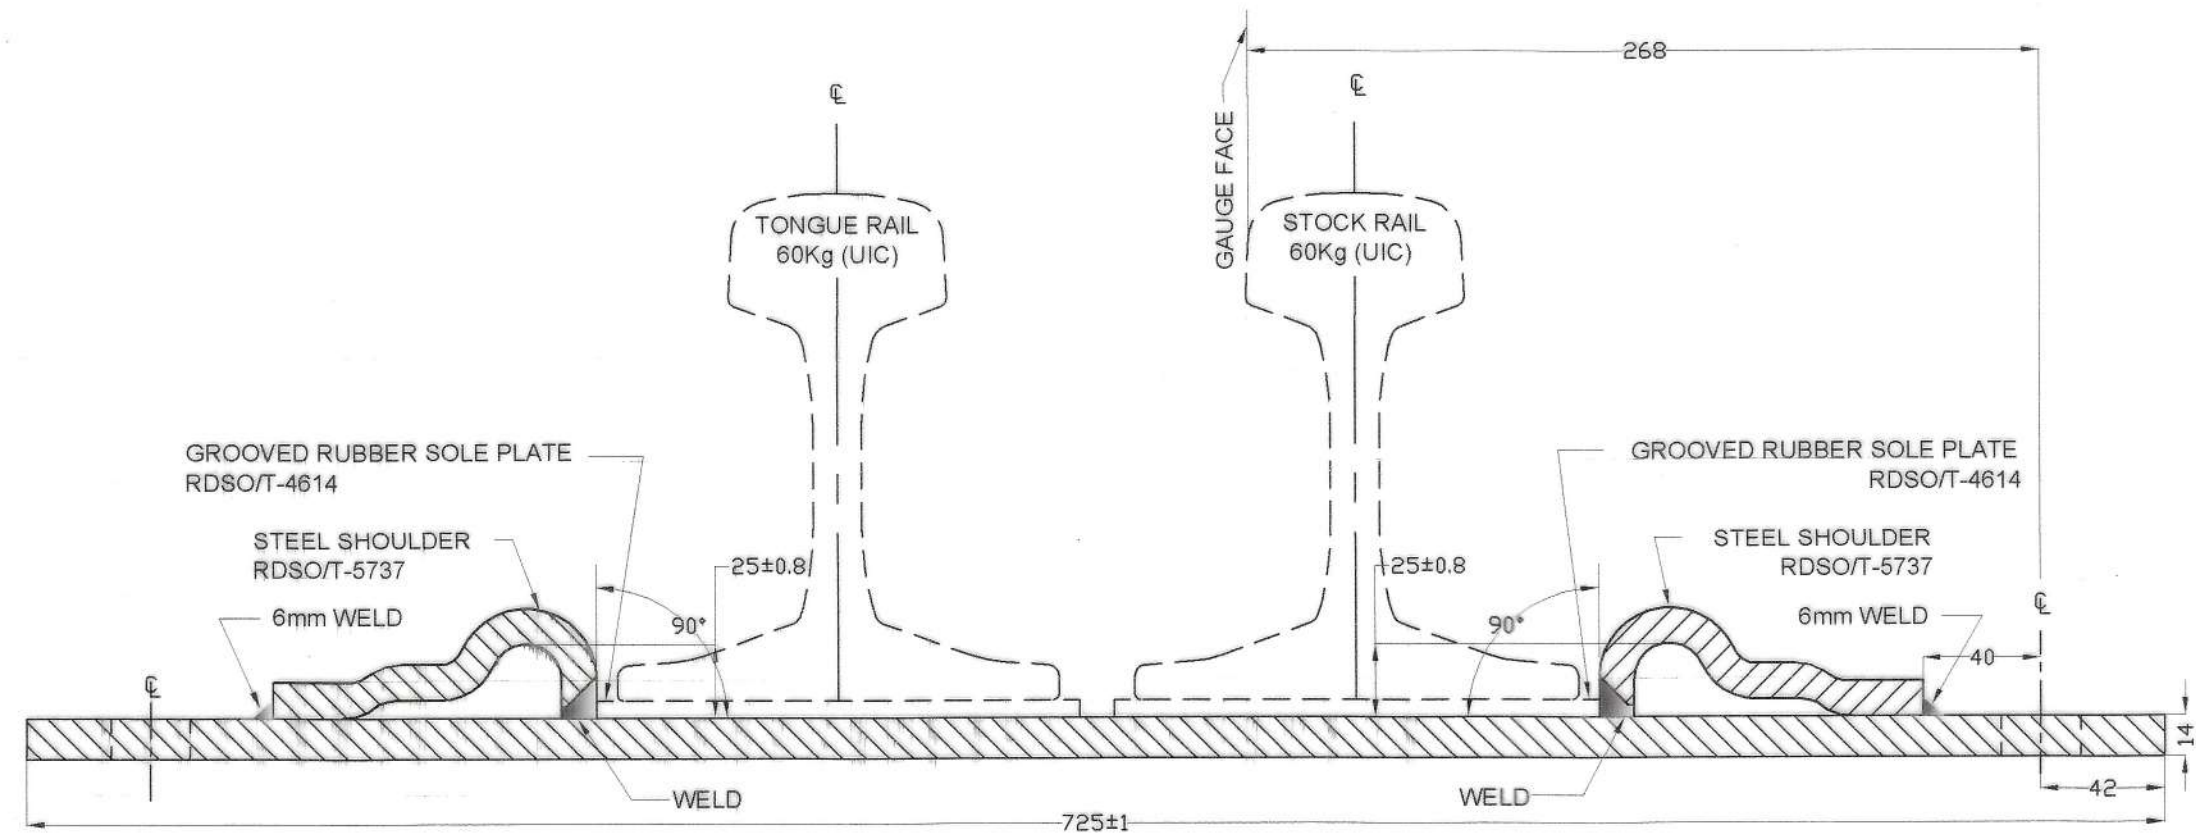

SECTIONAL ELEVATION ON 'AB'

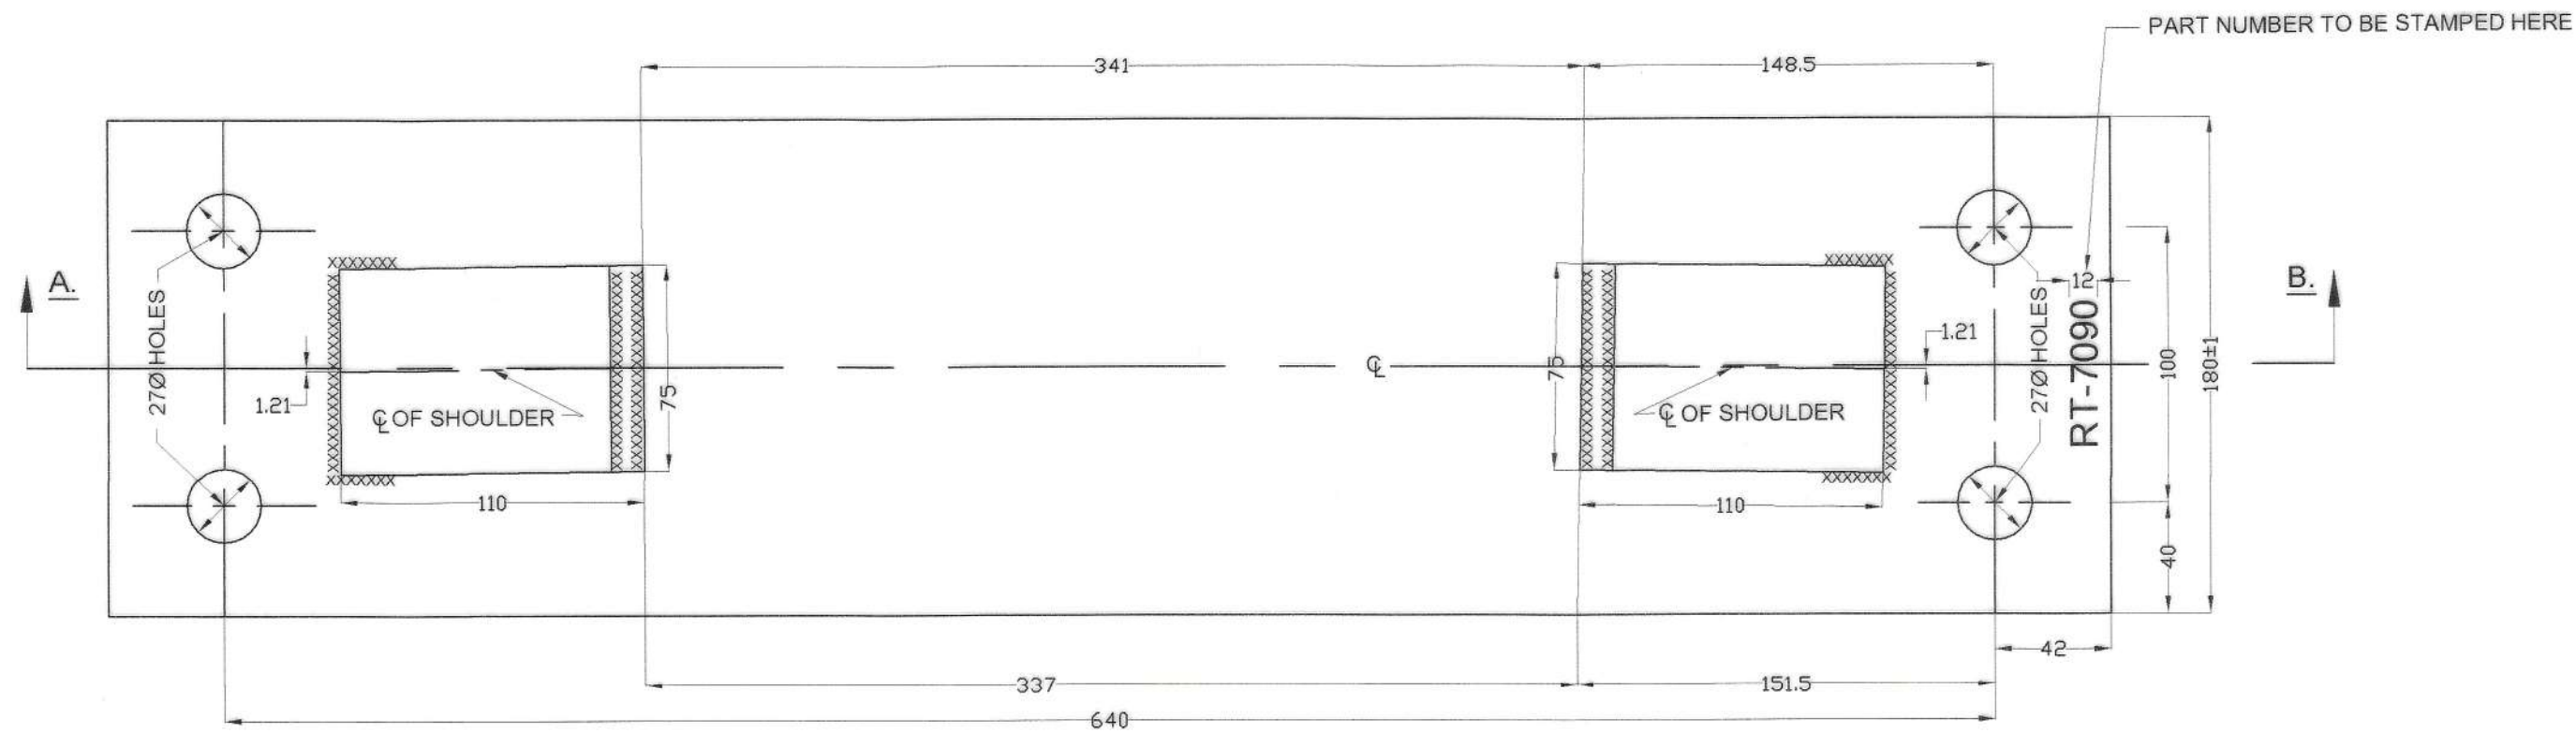

PLAN

THIS DRAWING IS THE PROPERTY OF
RESEARCH DESIGNS AND STANDARDS ORGANISATION
(MINISTRY OF RAILWAYS)
LUCKNOW-226011, INDIA
AND SHALL NOT BE USED, COPIED OR REPRODUCED IN
PART OR WHOLE, WITHOUT PRIOR CONSENT IN WRITING

R. D. S. O.

SPECIAL FLAT BEARING PLATE
FOR 11200 mm CURVED SWITCH
WITH ZU-1-60 THICK-WEB TONGUE
RAILS B.G. (1673 mm) FOR 60Kg (UIC)
ON P.S.C. SLEEPERS.

STAND: ADVANCE (T)
CANCELS: 29-01-2010
REV:

1. ALL DIMENSIONS ARE IN MILLIMETERS.
2. LATEST ALTERATION NUMBER SHALL BE CHECKED BEFORE PLACING ORDER.
3. A TOLERANCE OF 0.8 mm EACH WAY IS PERMITTED IN THE POSITION OF HOLES.

2. IS: 2062-1992
1. IRS WELDED BRIDGE CODE
FOR WELDING.

NOT TO SCALE

01

REVISED & REDRAWN

23-09-2021

NOTE

SPECIFICATION

SCALE

ALT:

DESCRIPTION

DATE

RDSO/T-7090