

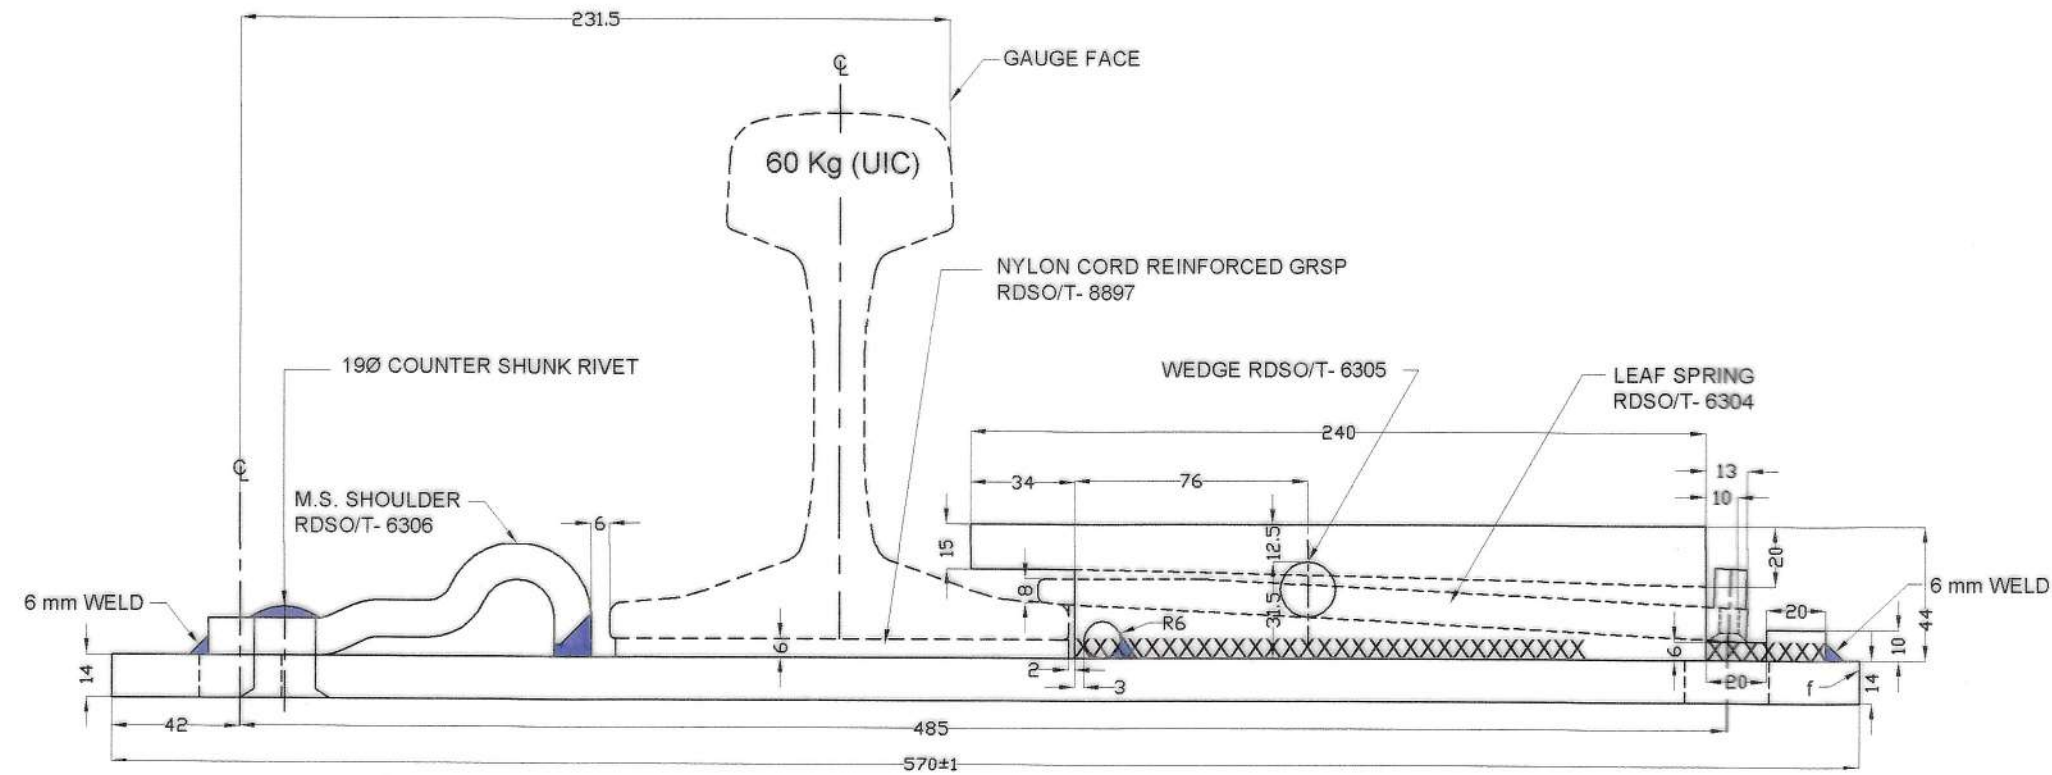


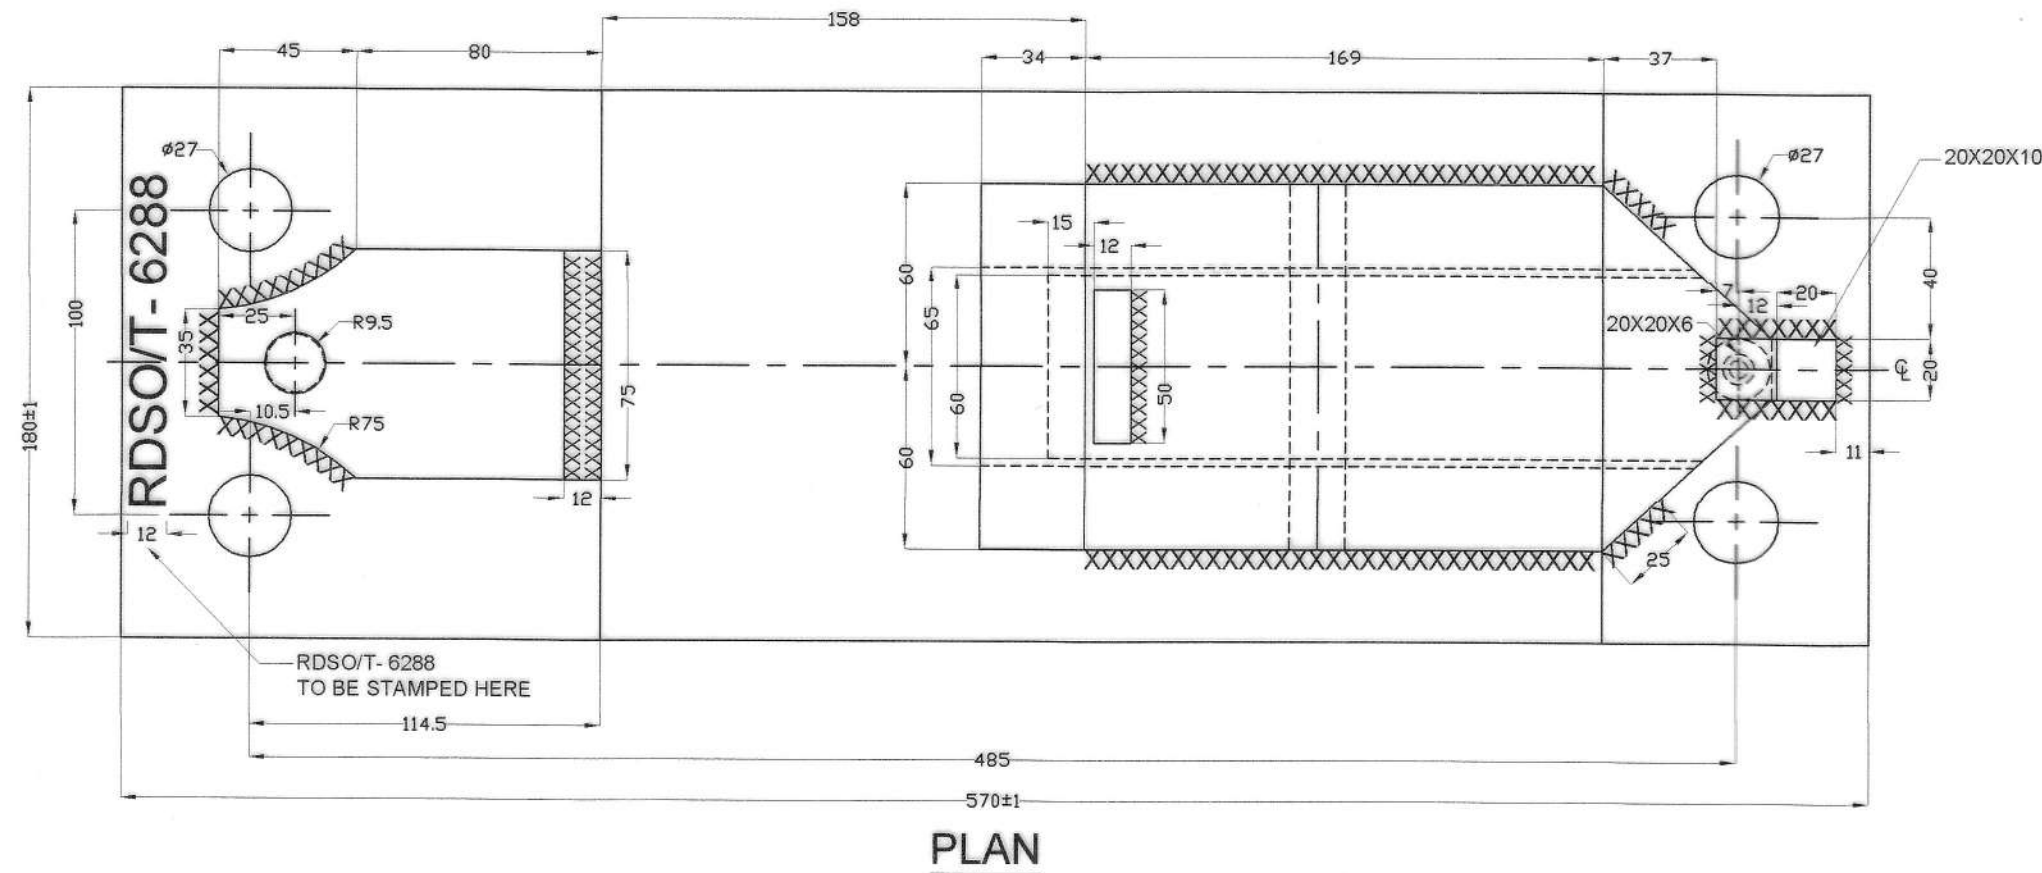

SECTIONAL ELEVATION ON A.B.

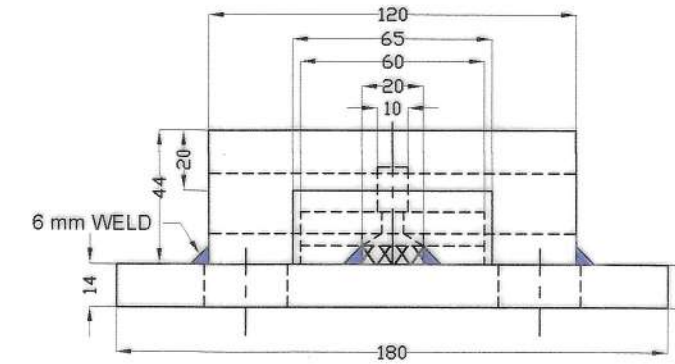

PLAN

5. MIG PROCESS OF WELDING TO BE ADOPTED.
4. THE SLIDE CHAIR SHALL BE FIXED BY MEANS OF FOUR PLATE SCREWS TO DRG. No. RDSO/T- 3912 THROUGH THE ROUND HOLES & SINGLE COIL SPRING WASHER TO DRG. No. T 10773.
3. A TOLERANCE 0.8 mm EACH WAY IS PERMITTED IN THE POSITION OF HOLES.
2. LATEST ALTERATION NUMBER SHALL BE CHECKED BEFORE PLACING ORDER.
1. ALL DIMENSIONS ARE IN MILLIMETRES.

NOTE

3. IRS: WELDED BRIDGE CODE FOR WELDING
2. IS:2062-1999, Gr. - B
1. IRS: T-10

SPECIFICATION

NOT TO SCALE

SCALE

1

ALT:

REVISED & REDRAWN
"GROOVED RUBBER SOLE PLATES"
REPLACE WITH "NYLON CORD
REINFORCED GRSP"

DESCRIPTION

20-09-2021

DATE

20 Nos.	6400 mm CURVED SWITCH FOR 1 IN 8.5 TURNOUT WITH ZU-1-60 THICK-WEB TONGUE RAILS B.G. (1673 mm) ON PSC SLEEPERS	RDSO/T- 6280
No. OFF	DESCRIPTION FOR DRAWING	No.
THIS DRAWING IS THE PROPERTY OF RESEARCH DESIGNS AND STANDARDS ORGANISATION (MINISTRY OF RAILWAYS) LUCKNOW-226011, INDIA AND SHALL NOT BE USED, COPIED OR REPRODUCED IN PART OR WHOLE, WITHOUT PRIOR CONSENT IN WRITING .		
R. D. S. O.		
SLIDE CHAIR FOR 6400 mm CURVED SWITCH WITH ZU-1-60 THICK-WEB TONGUE RAILS B.G. (1673 mm) FOR 60 Kg (UIC) ON P.S.C. SLEEPERS.		
STAND: _____	ADVANCE	(T)
CANCEL: _____	24-02-2004	
REV: _____	RDSO/T- 6288	