



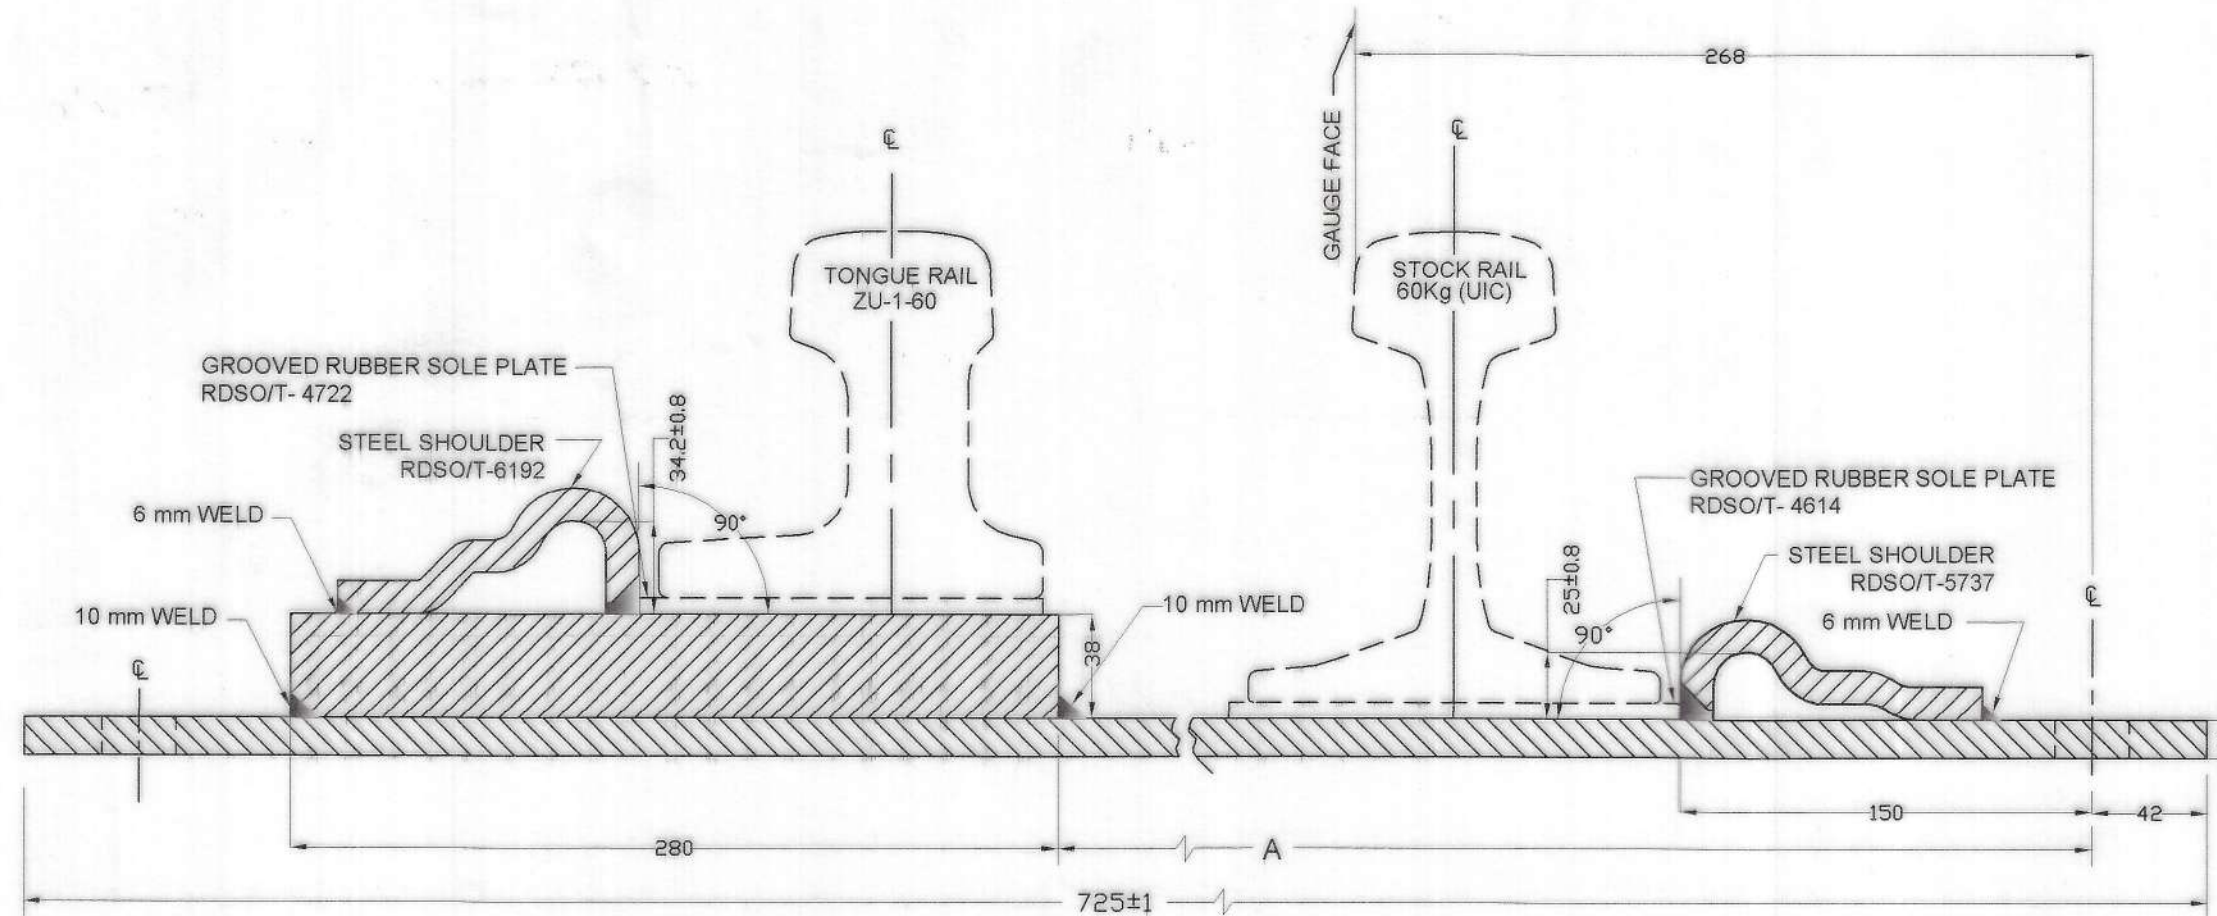

SECTIONAL ELEVATION ON 'AB'

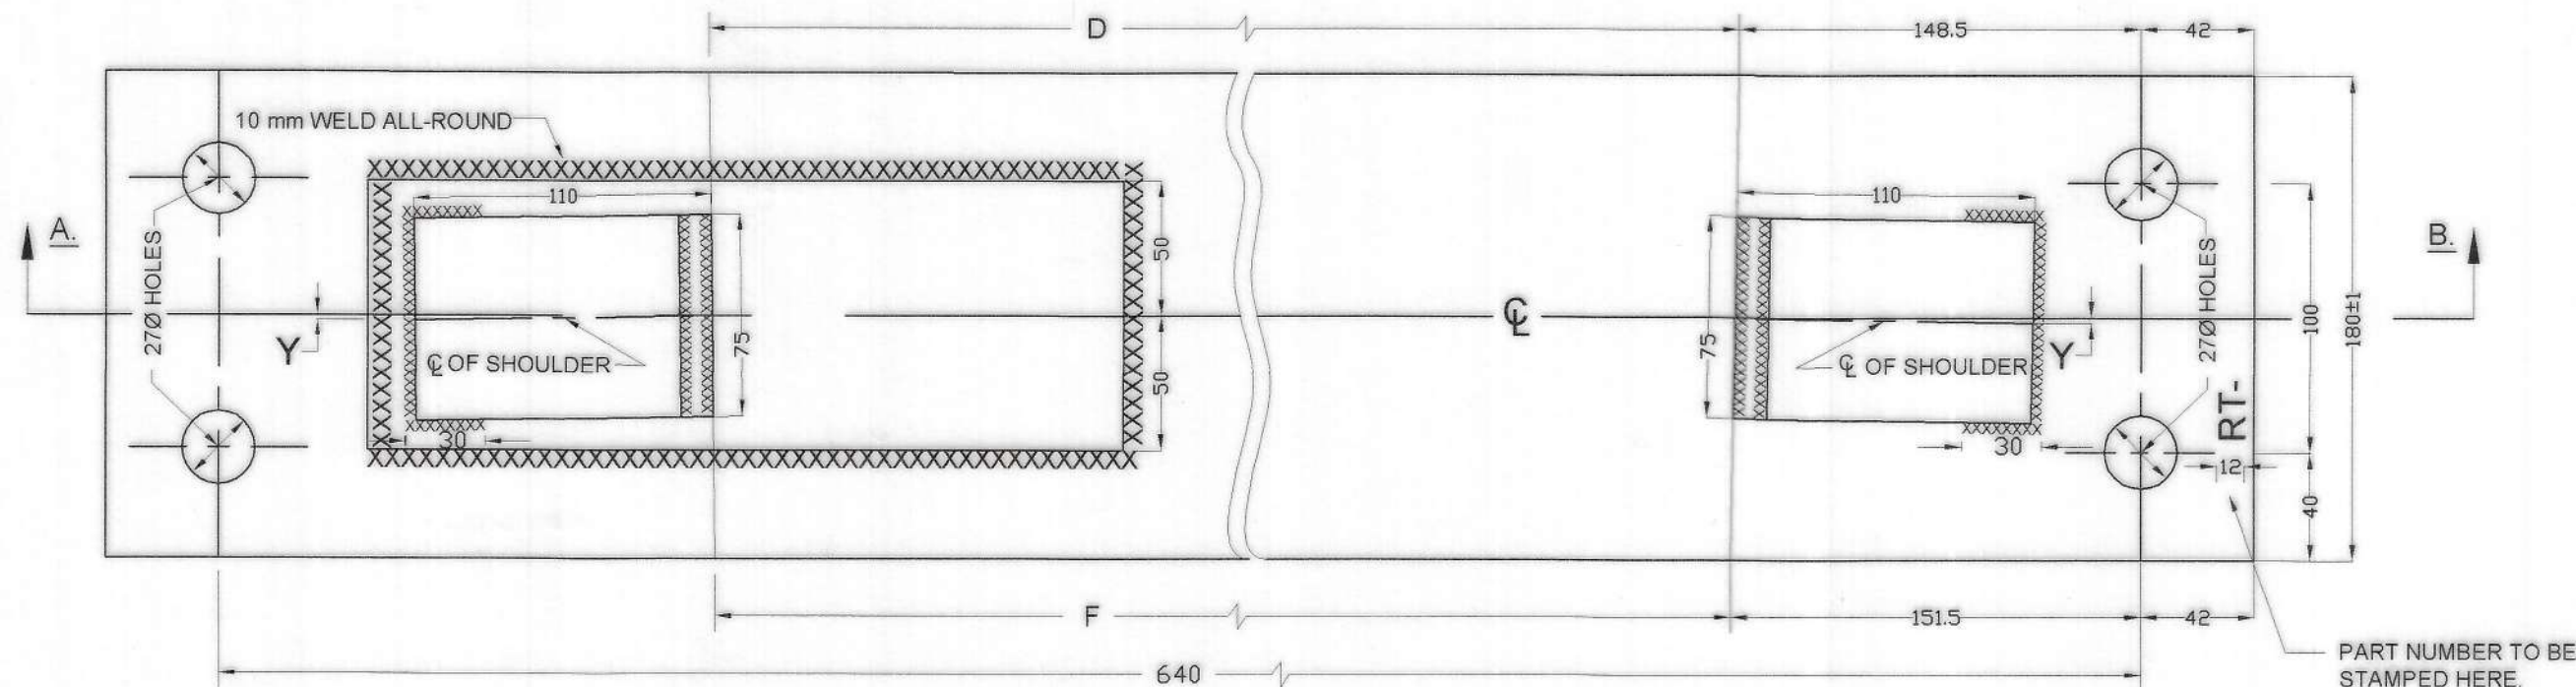

PLAN

4. DIMENSIONS GIVEN SHOWN WHERE THE CENTRE AND CROSS-LINES MEET THE EDGES OF THE BEARING PLATE.
3. A TOLERANCE OF 0.8 mm EACH WAY IS PERMITTED IN THE POSITION OF HOLES.
2. LATEST ALTERATION NUMBER SHALL BE CHECKED BEFORE PLACING ORDER.
1. ALL DIMENSIONS ARE IN MILLIMETERS.

NOTE

3. IRS. T-10.
2. IS: 2062-1999
1. IRS. WELDED BRIDGE CODE
FOR WELDING.

NOT TO SCALE

1.

REVISED & REDRAWN

23-09-2021

STAN: CANCELLED
REV: ADVANCE
29.01.2010

(T)

SPECIFICATION

SCALE

ALT:

DESCRIPTION

DATE

RDSO/T-7085 & RDSO/T-7086

TABLE OF DIMENSIONS

SLEEPER No.	PART No.	DIMENSIONS (mm)			
		Y	D	F	A
21	RDSO/T- 7085	1.12	325.5	322.0	322.0
22	RDSO/T- 7086	1.16	338.0	334.5	335.0