

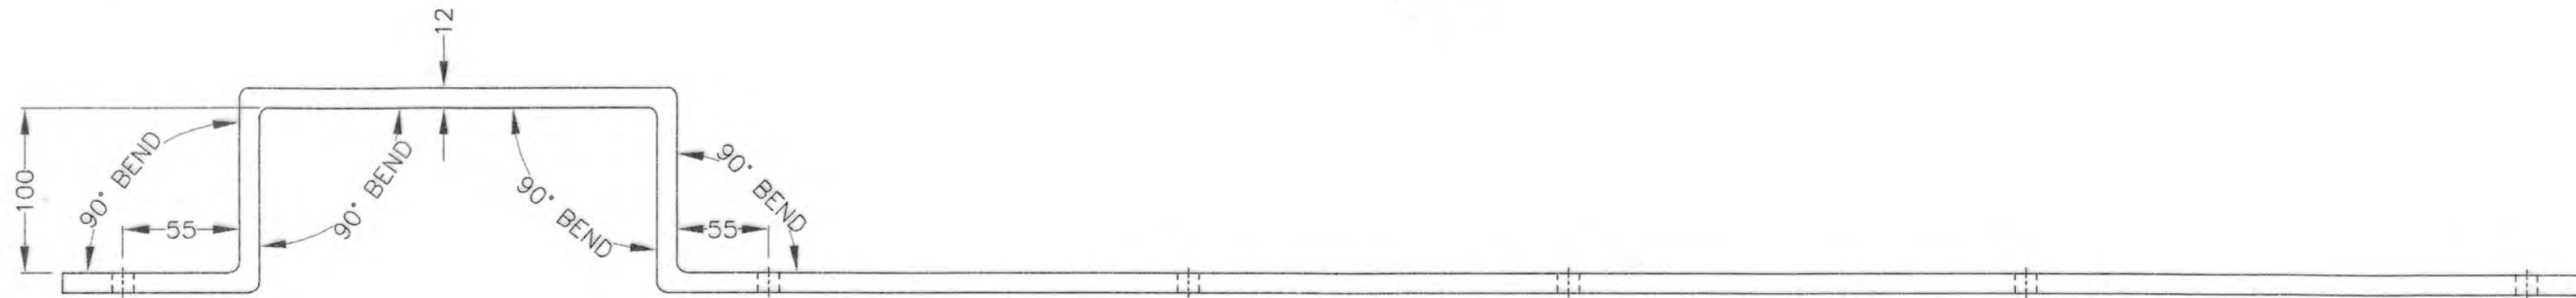
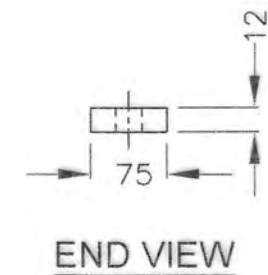
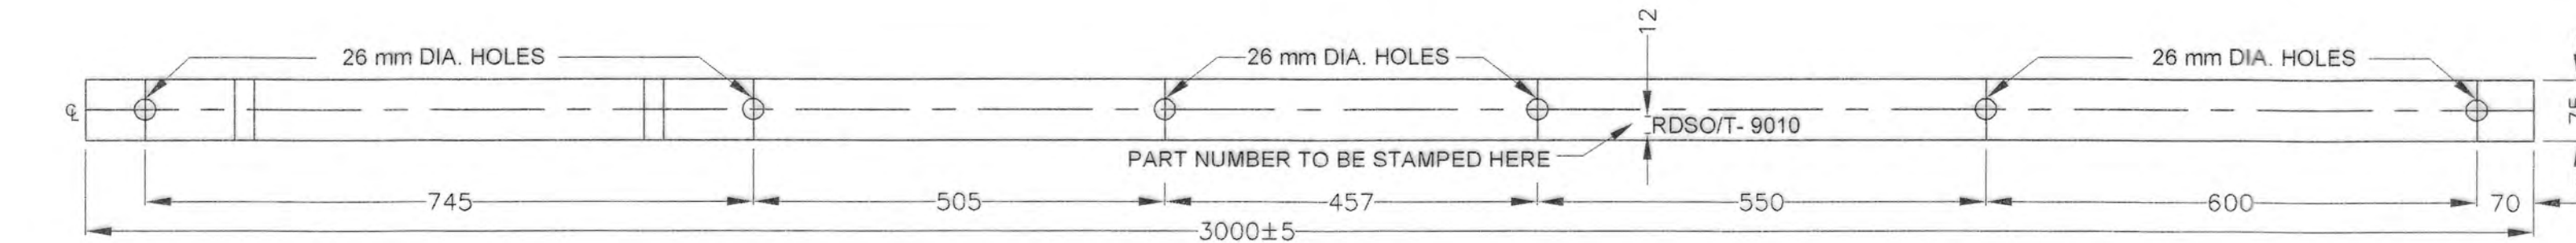


FILE n.p. No.	CT/PTX/TWS/Design n.p. No. 1 & 2 (S. No. 621 TO ----)	C.R. No. PAGES	DRG: BY:	M. K. MANDAL (SSE/T)	CH: BY:	ANURAG BAJPAL (JBT)	RAMMOHAN (SSE/T)	ADE/T/P&C	VIRPAL SINGH	APPD:	JDST-III	✓ AJAY KUMAR SHARMA
------------------	---	-------------------	-------------	-------------------------	------------	------------------------	---------------------	-----------	--------------	-------	----------	------------------------

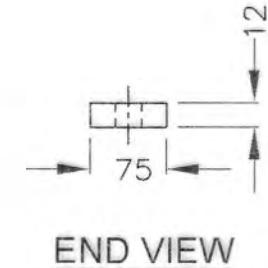

ELEVATION
(RDSO/T- 9010)

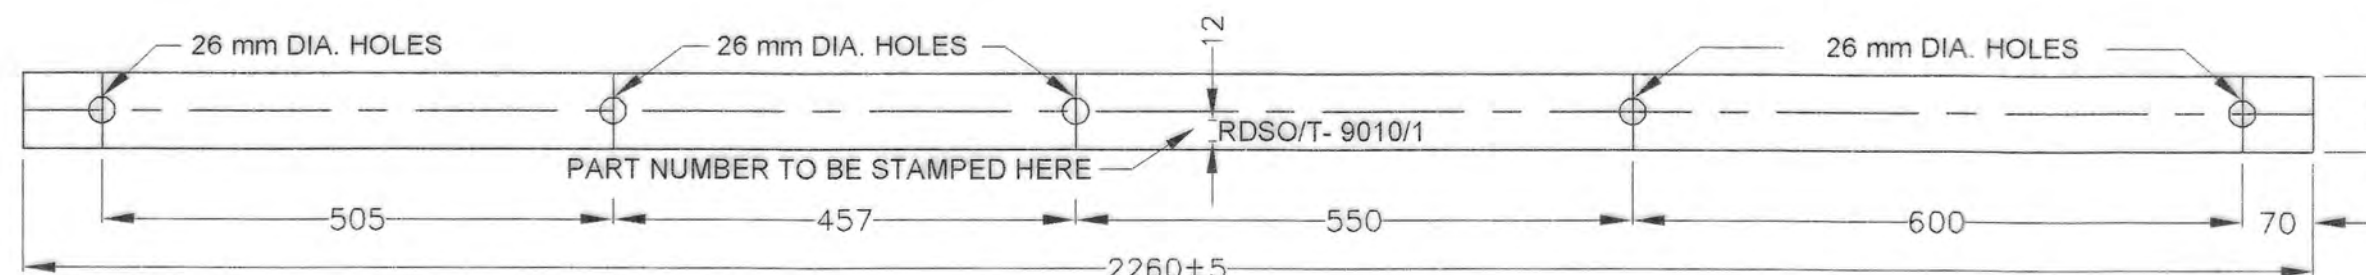

ELEVATION
(RDSO/T- 9010/1)

3. M.S. FLAT TIE BAR TO DRG. No. RDSO/T- 9010 SHALL BE USED ON NON POINT MACHINE END AT SLEEPER No. 2AS, 1AS, 1, 2, 3 & 4 AND M.S. FLAT TIE BAR TO DRG. No. RDSO/T- 9010/1 SHALL BE USED ON POINT MACHINE END AT SLEEPER No. 2AS, 1AS, 1, 2 & 3 AS SHOWN ON LAYOUT OF TURNOUT.
2. LATEST ALTERATION No. SHALL BE CHECKED BEFORE PLACING ORDER.
1. ALL DIMENSIONS ARE IN MILLIMETERS.

NOTE

IS: 226

NOT TO SCALE

01

REVISED & REDRAWN

12-10-2023

BEND PROVIDED IN
RDSO/T- 9010

STAND. _____
CANC. _____
REV. _____

ADVANCE
27-06-2022

(T)

SPECIFICATION

SCALE

ALT:

DESCRIPTION

DATE

RDSO/T- 9010 & RDSO/T- 9010/1