

Signature

AJAY KUMAR SHARMA

JDST-III

APPD:

Signature

VIRPAL SINGH

ADE/T/P&C

Signature

RAMMOHAN (SSE/T)

Signature

R. P. VERMA (SSE/T)

CHECK: BY:

Signature


M. K. MANDAL (SSE/T)

DRG: BY:


C.R.No. PAGES

CT/PTX/TWS/Design n.p no. 1&2 (S. No. 821 TO)


FILE S.No.

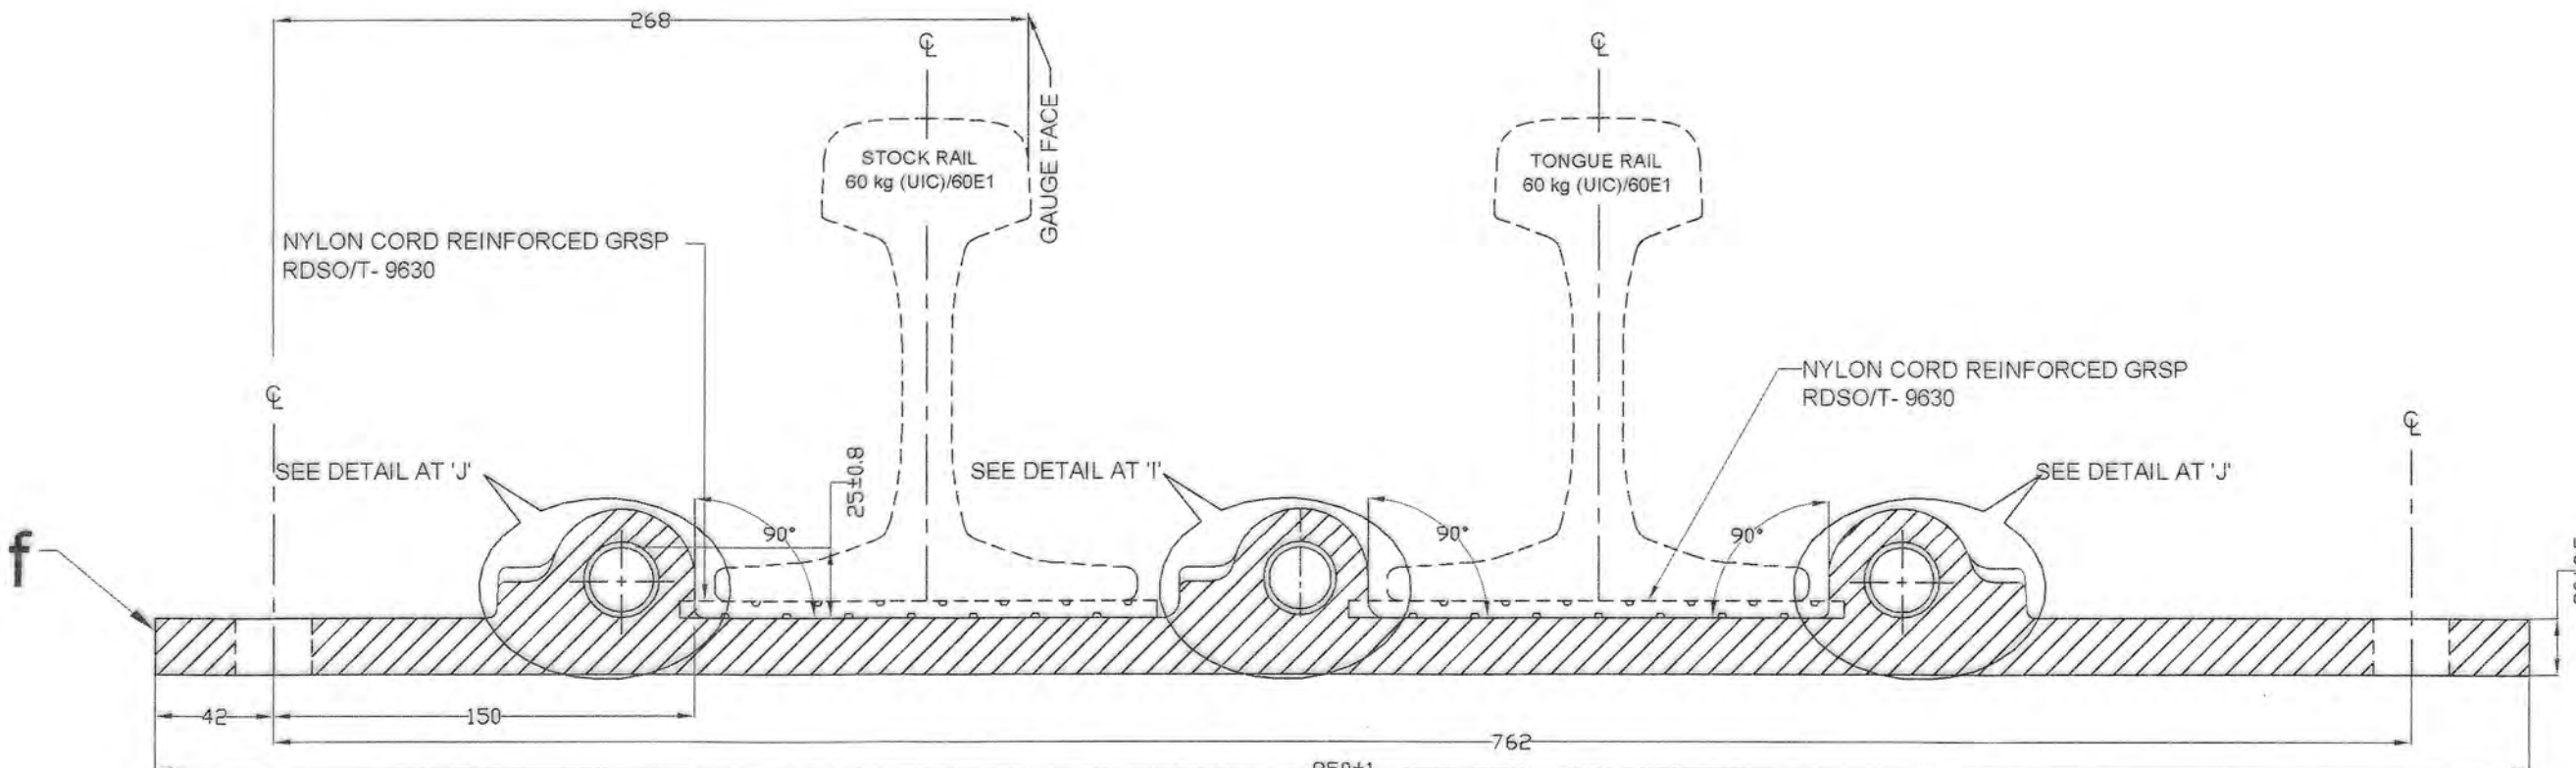


SECTIONAL ELEVATION ON GH

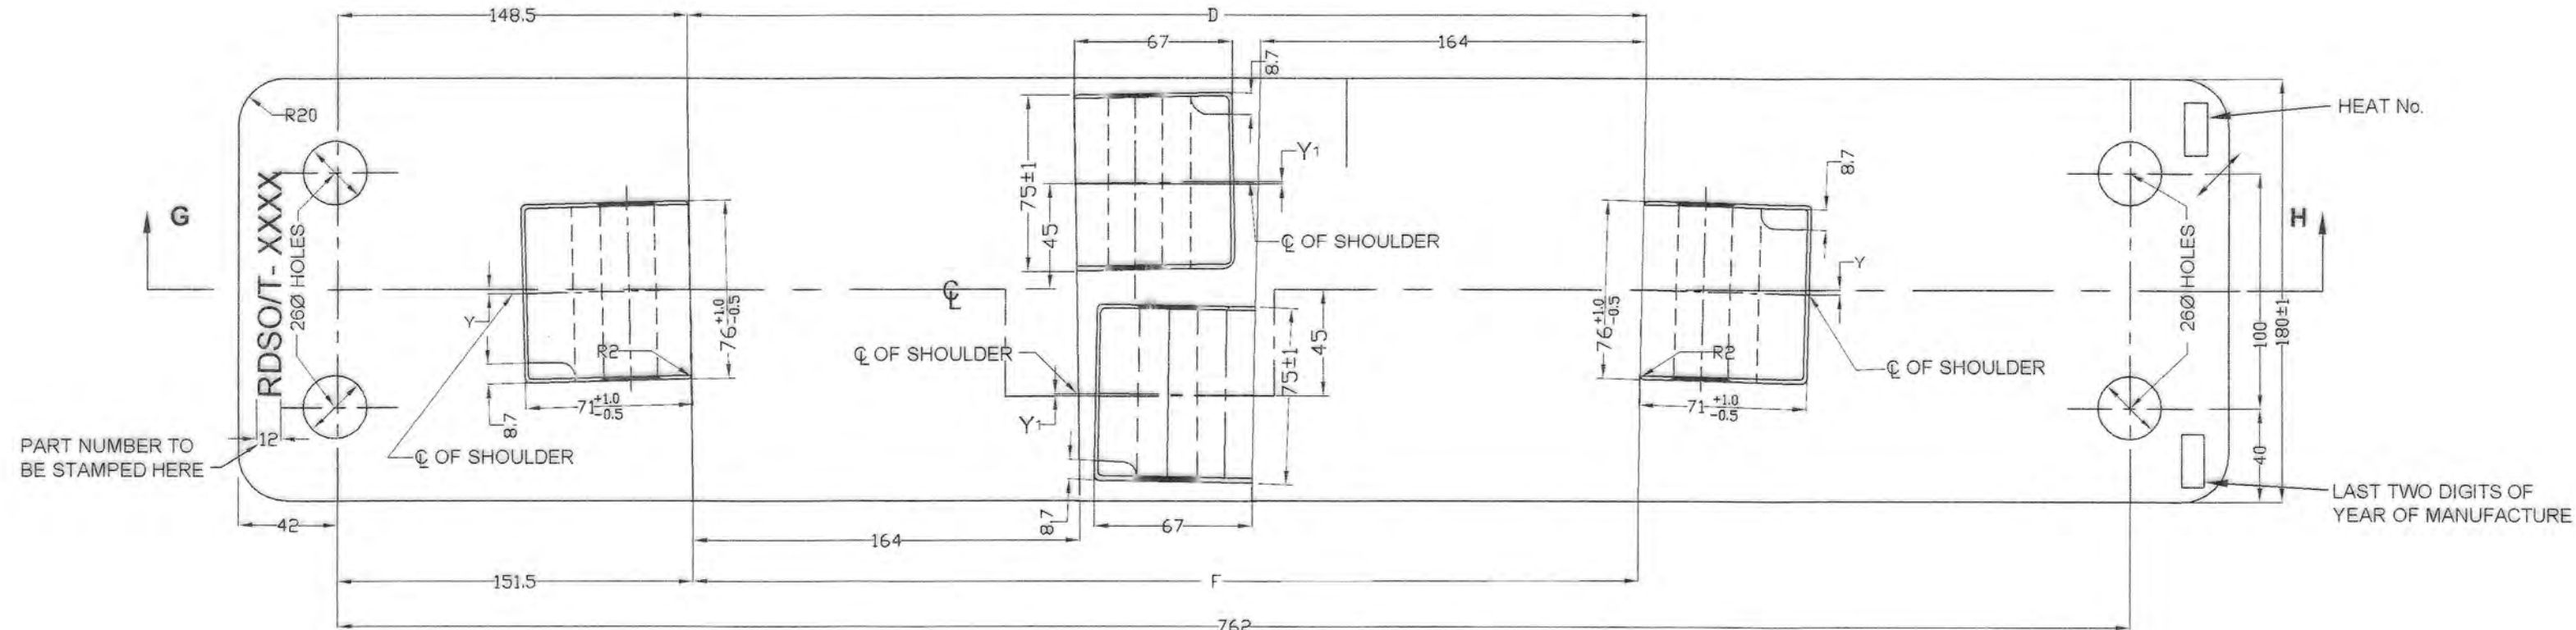

PLAN

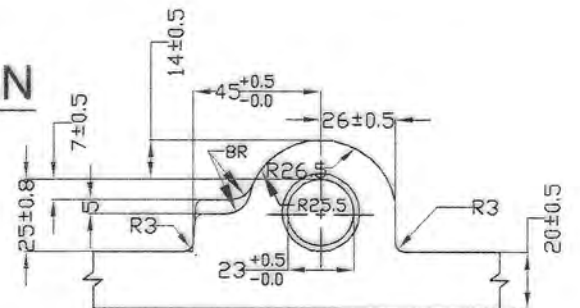

DETAIL 'J'

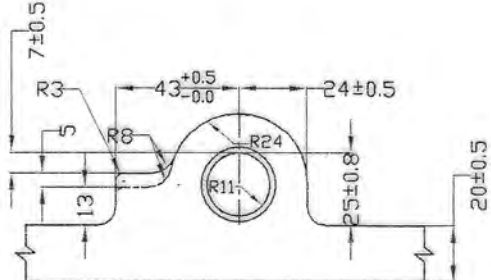

DETAIL 'I'

8. MACHINED SURFACE SHOWN THUS ----- f.
7. THE SPECIAL FLAT BEARING PLATE SHALL BE FIXED BY MEANS OF FOUR PLATE SCREWS TO DRG. No. RDSO/T- 3913 THROUGH THE ROUND HOLES & SINGLE COIL SPRING WASHER TO DRG. No. T 10773.
6. ALL MARKING SHALL BE IN 12 MM SIZE IN RAISED LETTERS.
5. ALL THE SHARP EDGES ARE TO BE MADE BLUNT WITH 3R PREFERABLY, EXCEPT WHERE OTHERWISE SHOWN.
4. DIMENSION GIVEN SHOW WHERE THE CENTRE AND CROSS-LINES MEET THE EDGES OF THE BEARING PLATE.
3. A TOLERANCE OF 0.8 mm EACH WAY IS PERMITTED IN THE POSITION OF HOLES.
2. LATEST ALTERATION NUMBER SHALL BE CHECKED BEFORE PLACING ORDER.
1. ALL DIMENSIONS ARE IN MILLIMETRES.

NOTE

TABLE OF DIMENSIONS

SLEEPER NO.	PART NO.	DIMENSIONS (mm)			
		D	F	Y	Y ₁
25	RDSO/T- 9627	407	401	1.84	1.12
26	RDSO/T- 9628	425.5	419.5	1.91	1.16
27	RDSO/T- 9629	445	438.5	1.98	1.21

ONE EACH

10125 mm CURVED SWITCH WITH ZU-1-60/ 60E1A1 THICK - WEB TONGUE RAIL FOR 1 IN 12 TURNOUT B.G. (1673 mm) FOR 60 KG (UIC)/60E1 ON PSC SLEEPERS

RDSO/T- 6155

No. OFF

DESCRIPTION FOR DRAWING

No.

THIS DRAWING IS THE PROPERTY OF RESEARCH DESIGNS AND STANDARDS ORGANISATION (MINISTRY OF RAILWAYS) LUCKNOW-226011, INDIA AND SHALL NOT BE USED, COPIED OR REPRODUCED IN PART OR WHOLE, WITHOUT PRIOR CONSENT IN WRITING.

R. D. S. O.

CAST STEEL SPECIAL FLAT BEARING PLATES FOR 10125 mm CURVED SWITCH WITH ZU-1-60/60E1A1 THICK-WEB TONGUE RAILS B.G. (1673 mm) FOR 60 kg(UIC)/ 60E1 ON P.S.C. SLEEPERS.

STAND: ADVANCE 12-10-2023
CANC: (T)
REV: RDSO/T- 9627 TO RDSO/T- 9629

IS 1030:1998 (Reaffirmed 2022)
GRADE: 280-520 W

NOT TO SCALE

SPECIFICATION	SCALE	ALT:	DESCRIPTION	DATE
---------------	-------	------	-------------	------