

FILE S.No.	CT/PTX/TWS/Design n.p. 01 To 04 FILE S. No. 530 TO	C.R. No. PAGES	DRG: BY: S.K. SAGAR (SSE/T)	DRG: CH: R.P. VERMA (SSE/T)	RAMMOHAN (SSE/T)	ADE/T/P&C	VIRPAL SINGH	APPD:	DST-III	SACHIN VERMA
------------	--	----------------	-----------------------------	-----------------------------	------------------	-----------	--------------	-------	---------	--------------

2. LATEST ALTERATION No. SHALL BE CHECKED BEFORE PLACING ORDER.
1. ALL DIMENSIONS ARE IN MILLIMETRES.

INDIAN RAILWAY STANDARDS
SPECIFICATION FOR 6 mm THICK NYLON
CORD REINFORCED GROOVED
RUBBER SOLE PLATE FOR PLACING
BENEATH RAILS AT TURNOUTS
(PROVISIONAL) - 2020 (Revision 1.0)
No. RDSO/M&C/RP - 201/2020 (Revision 1.0)

NOT TO SCALE

THIS DRAWING IS THE PROPERTY OF
RESEARCH DESIGNS AND STANDARDS ORGANISATION
(MINISTRY OF RAILWAYS)
LUCKNOW - 226011, INDIA
AND SHALL NOT BE USED, COPIED OR REPRODUCED IN
PART OR WHOLE, WITHOUT PRIOR CONSENT IN WRITING.


R. D. S. O.

6 mm THICK NYLON CORD
REINFORCED GROOVED
RUBBER SOLE PLATES WITH
HORNS


STAND:-----
CANC LD:-----
REV D:-----
ADVANCE
09-03-2023

(T)


RDSO/T- 9630

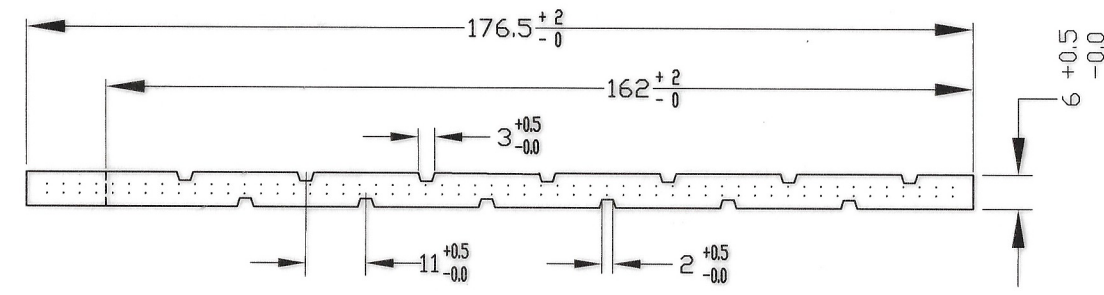


ELEVATION

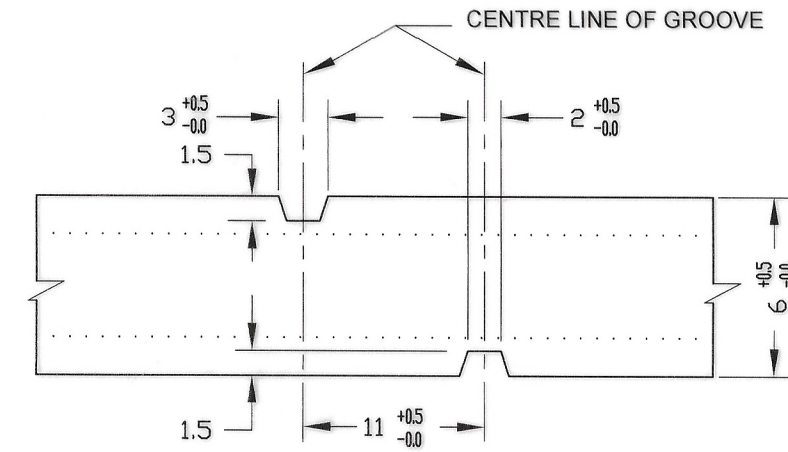

DETAIL OF GROOVES

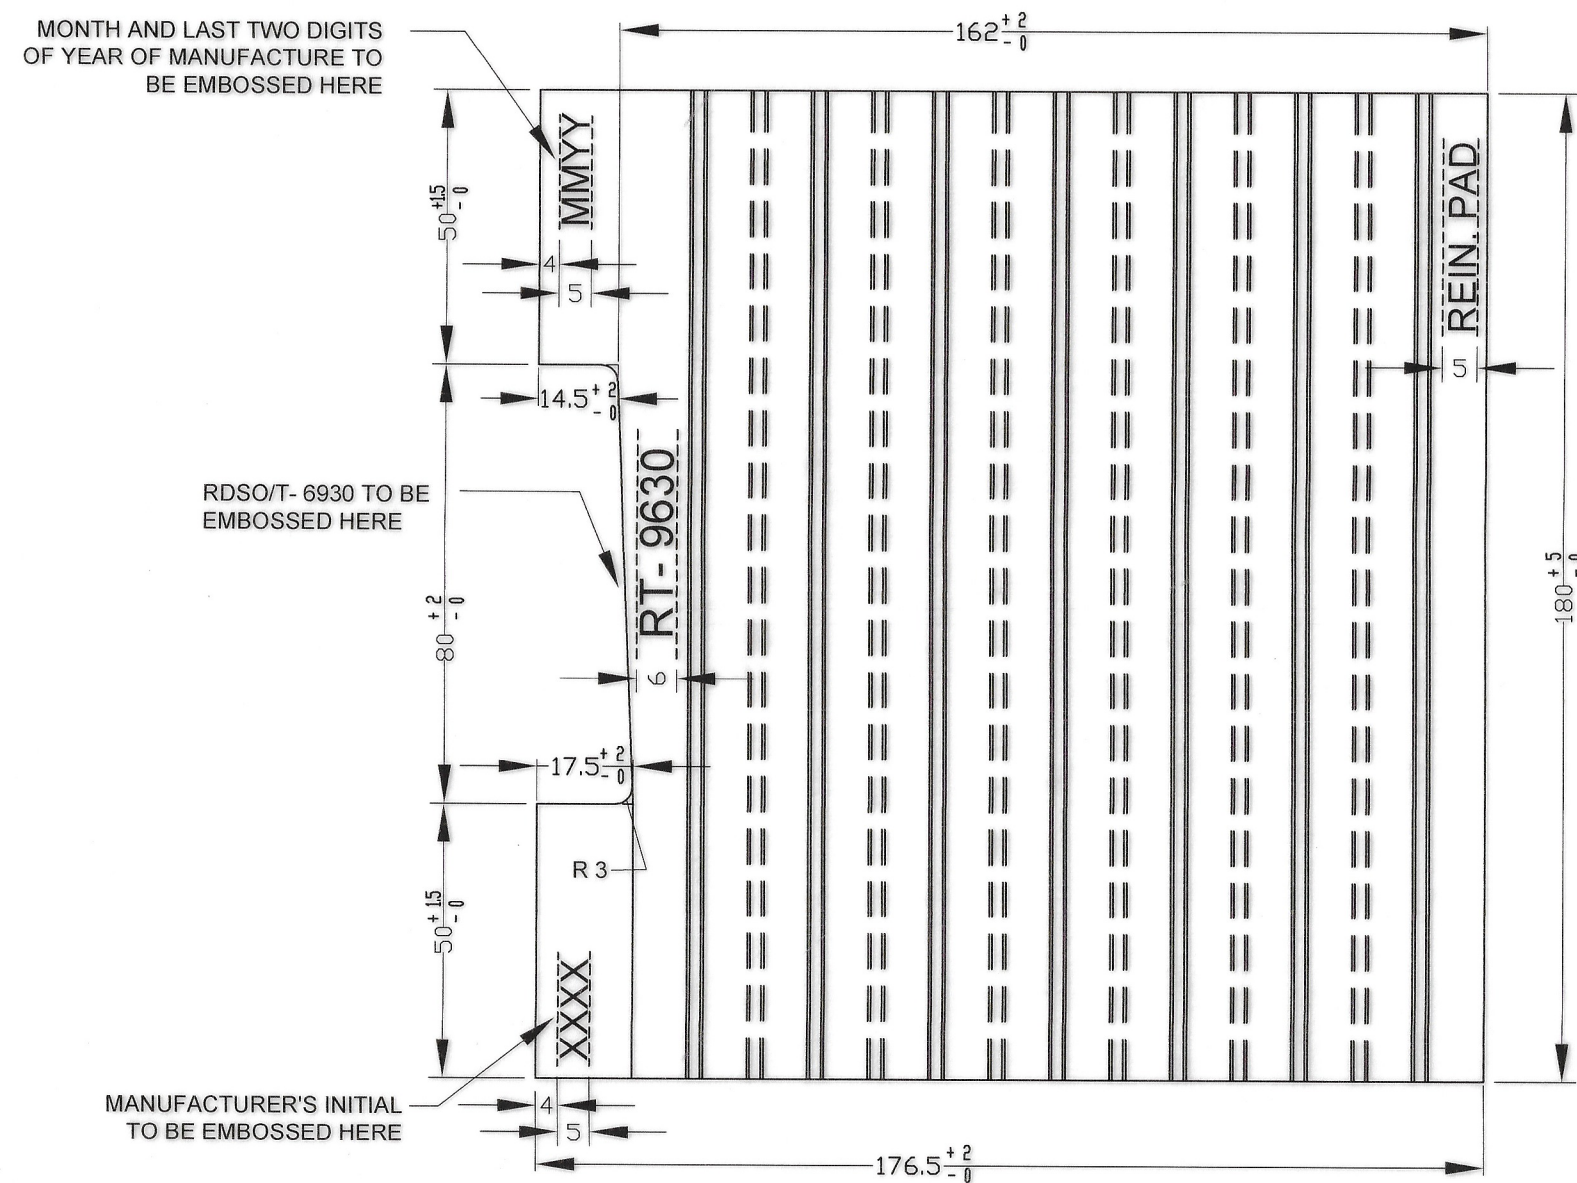

PLAN

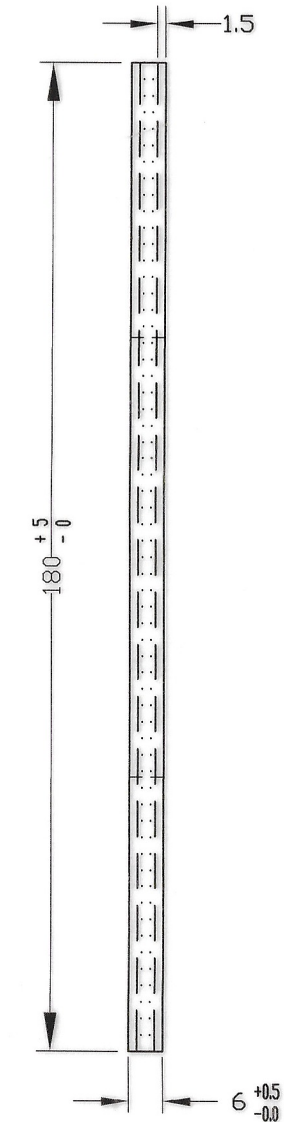

SIDE ELEVATION