


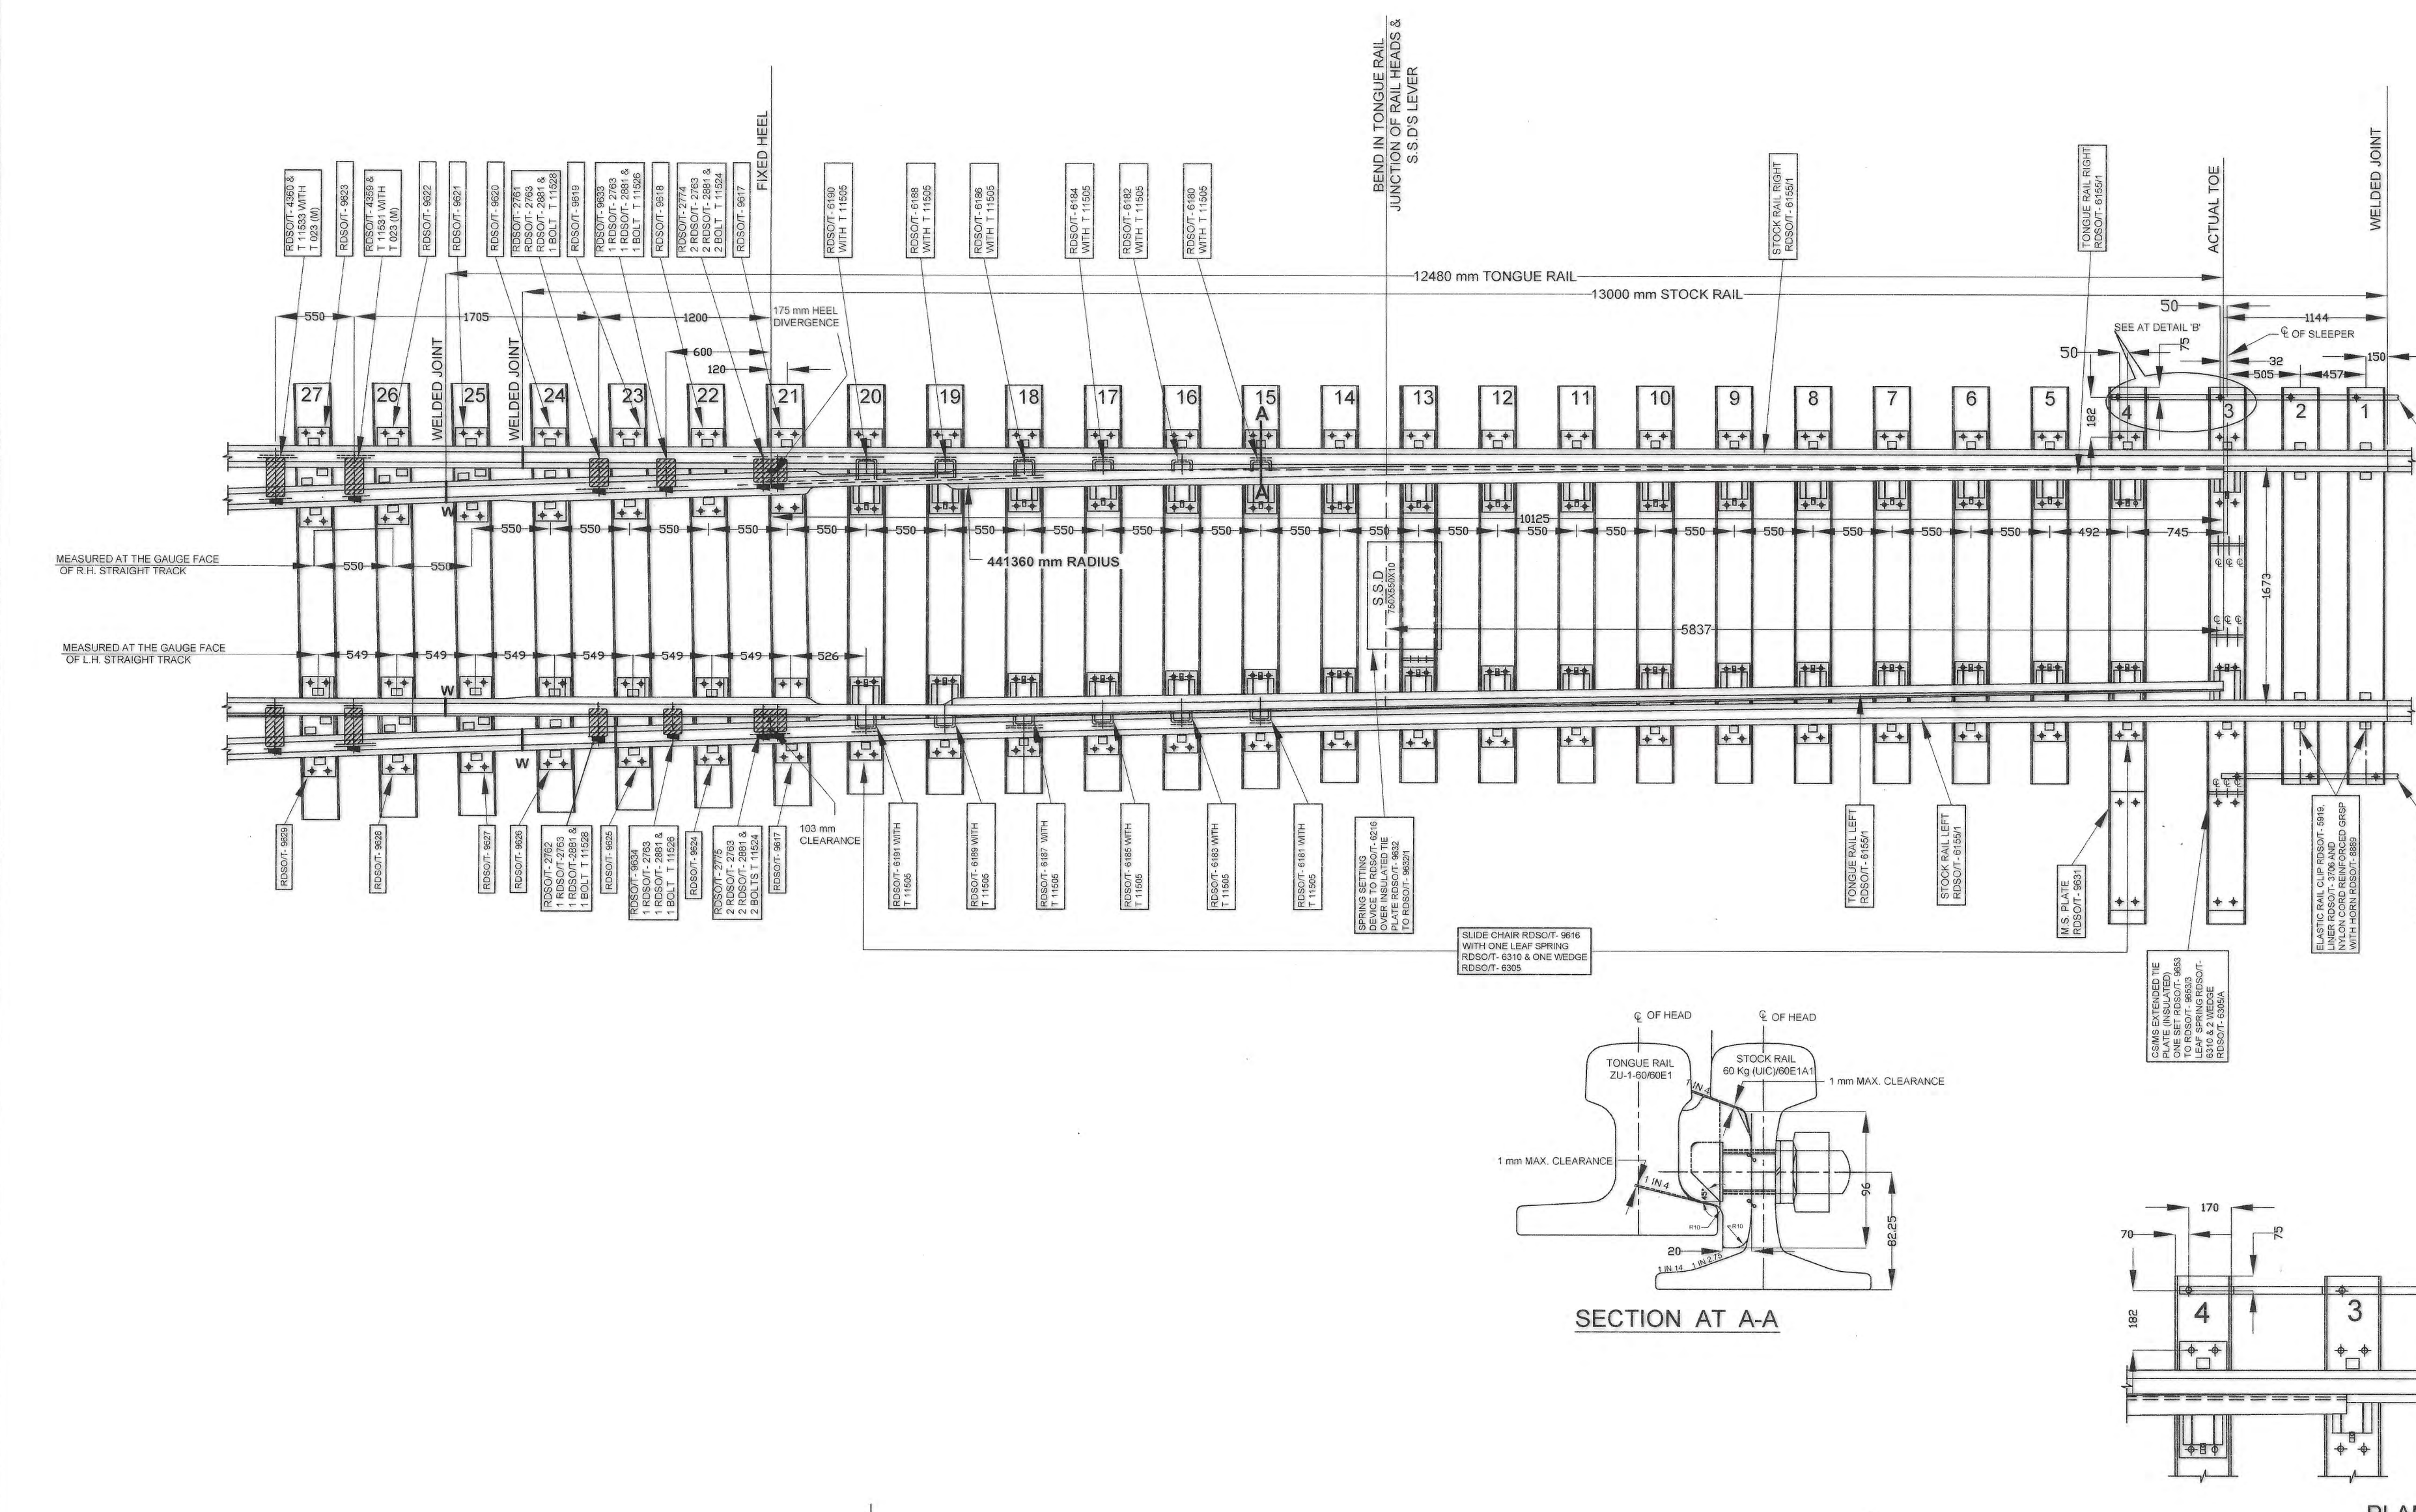

SWITCH ANGLE AT TOE-----0°- 20' - 0"

DIVERGENCE AT HEEL----- 175 mm

THROW AT TOE -----160 mm




GAUGE-----1673 mm

RADIUS-----441360 mm

TABLE OF SLEEPERS AND THEIR FITTINGS

S. No. OF SLEEPER	SLEEPER TO DRG. No.	LENGTH (mm)	INSULATED TIE PLATE ONE SET WITH FITTINGS	NO. OF NYLON CORD REINFORCED GRSP TO DRG. No. RDSOIT-		24 DIA. PLATE SCREWS RDSOIT- 3913	INSULATING LINERS RDSOIT- 3706	TWO NO. SLIDE CHAIRS	SINGLE COIL SPRING WASHER T 10773	M.S. PLATE RDSOIT- 9631	WEDGE TO DRG. No. RDSOIT- 6310	LEAF SPRING RDSOIT- 6310	METAL LINERS RDSOIT- 3740	ELASTIC RAIL CLIP M.K.V. RDSOIT- 9819
				8893	8894/ 8955									
1 & 2	RDSOIT- 4512	2750	RDSOIT- 9853 TO RDSOIT- 9853/3	-	-	4 (8899)	2 EACH	4 EACH	-	-	-	-	-	4 EACH
3	RDSOIT- 4514	3750	-	2	2 (8954)	2 (8906)	14	-	14	-	-	2	2	2
4	RDSOIT- 4515	3750	-	2	2 (8955)	2 (8906)	13	-	RDSOIT- 9616	13	1	2	-	2
5	RDSOIT- 4516	2750	-	2	2 (8955)	-	8	-	RDSOIT- 9616	8	-	2	-	2
6	RDSOIT- 4517	2750	-	2	2 (8955)	-	8	-	RDSOIT- 9616	8	-	2	-	2
7	RDSOIT- 4518	2750	-	2	2 (8955)	-	8	-	RDSOIT- 9616	8	-	2	-	2
8	RDSOIT- 4519	2750	-	2	2 (8955)	-	8	-	RDSOIT- 9616	8	-	2	-	2
9	RDSOIT- 4520	2750	-	2	2 (8955)	-	8	-	RDSOIT- 9616	8	-	2	-	2
10	RDSOIT- 4521	2750	-	2	2 (8955)	-	8	-	RDSOIT- 9616	8	-	2	-	2
11	RDSOIT- 4522	2750	-	2	2 (8955)	-	8	-	RDSOIT- 9616	8	-	2	-	2
12	RDSOIT- 4523	2750	-	2	2 (8955)	-	8	-	RDSOIT- 9616	8	-	2	-	2
13	RDSOIT- 4524	2750	RDSOIT- 9832 TO RDSOIT- 9832/1	2	2 (8955)	-	8	-	RDSOIT- 9616	8	-	2	-	2
14	RDSOIT- 4525	2750	-	2	2 (8955)	-	8	-	RDSOIT- 9616	8	-	2	-	2
15	RDSOIT- 4526	2750	-	2	2 (8955)	-	8	-	RDSOIT- 9616	8	-	2	-	2
16	RDSOIT- 4527	2750	-	2	2 (8955)	-	8	-	RDSOIT- 9616	8	-	2	-	2
17	RDSOIT- 4528	2750	-	2	2 (8955)	-	8	-	RDSOIT- 9616	8	-	2	-	2
18	RDSOIT- 4529	2770	-	2	2 (8955)	-	8	-	RDSOIT- 9616	8	-	2	-	2
19	RDSOIT- 4530	2750	-	2	2 (8955)	-	8	-	RDSOIT- 9616	8	-	2	-	2
20	RDSOIT- 4531	2800	-	2	2 (8955)	-	8	-	RDSOIT- 9616	8	-	2	-	2

S. No. OF SLEEPER	SLEEPER TO DRG. No.	LENGTH (mm)	SPECIAL FLAT BEARING PLATE TO DRG. No.	24 DIA. PLATE SCREWS TO DRG. No. RDSOIT- 3913		METAL LINERS RDSOIT- 3740	ELASTIC RAIL CLIP M.K.V. RDSOIT- 9819	SINGLE COIL SPRING WASHER T 10773	NYLON CORD REINFORCED GRSP RDSOIT-		
				RIGHT	LEFT				8897	8894	8895
21	RDSOIT- 4532	2820	RDSOIT- 9617	RDSOIT- 9617	8	2	2	8	2	2	2
22	RDSOIT- 4533	2830	RDSOIT- 9618	RDSOIT- 9618	8	4	4	8	2	2	2
23	RDSOIT- 4534	2850	RDSOIT- 9619	RDSOIT- 9619	8	4	4	8	2	2	2
24	RDSOIT- 4535	2970	RDSOIT- 9620	RDSOIT- 9620	8	6	6	8	2	2	2
25	RDSOIT- 4536	2880	RDSOIT- 9621	RDSOIT- 9621	8	8	8	8	-	2	4
26	RDSOIT- 4537	2900	RDSOIT- 9622	RDSOIT- 9622	8	8	8	8	-	2	4
27	RDSOIT- 4538	2920	RDSOIT- 9623	RDSOIT- 9623	8	8	8	8	-	2	4

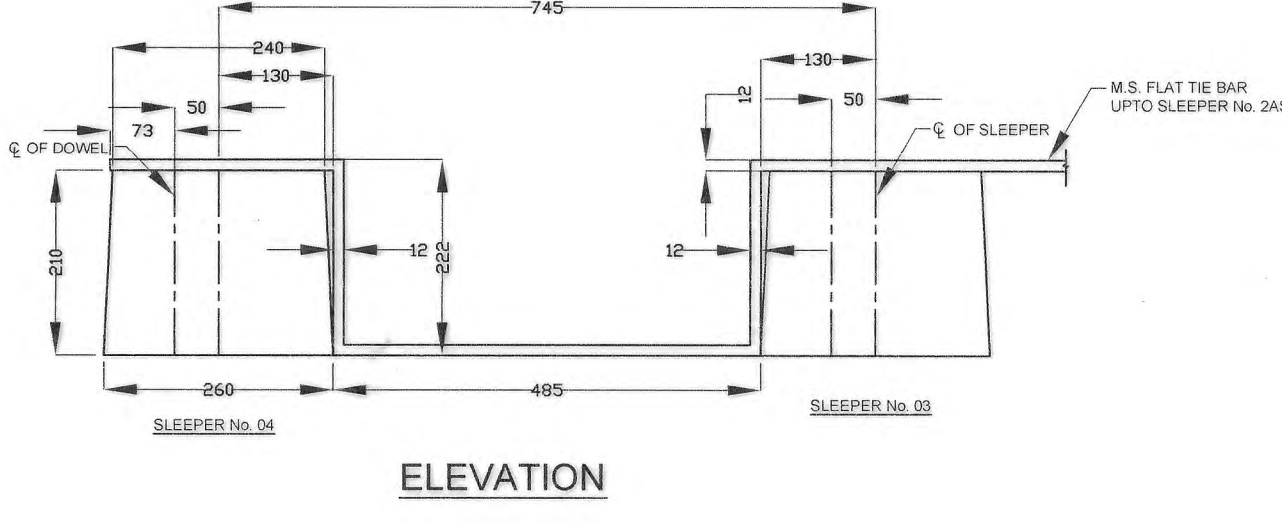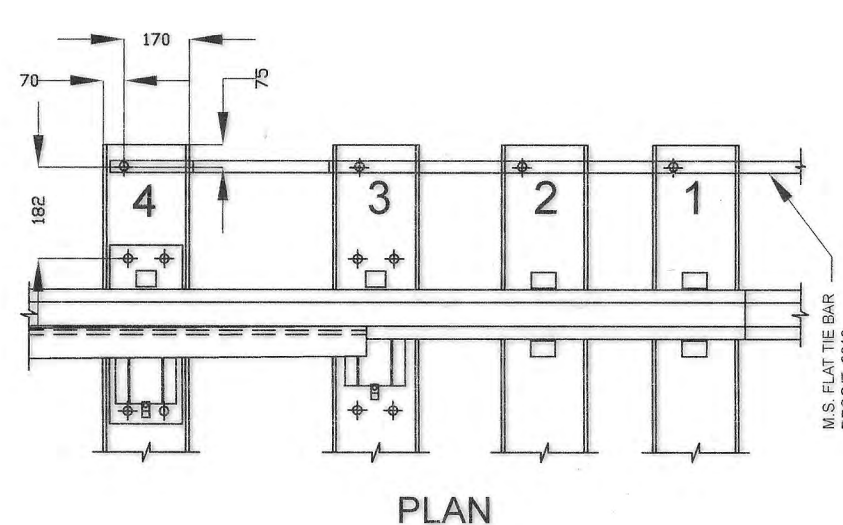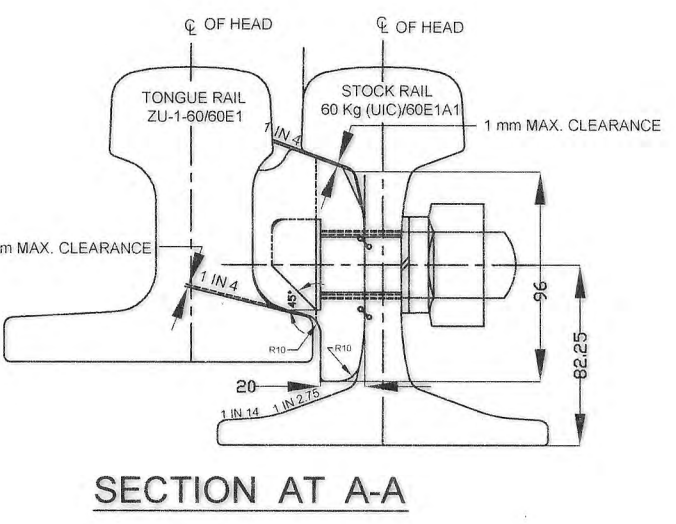

DETAIL 'B'
ARRANGEMENT OF M.S. FLAT TIE BAR AT SLEEPER No. 03 & 04

14. THE HEAD, WEB AND FOOT OF EACH RAIL SHALL BE ULTRASONICALLY TESTED BY THE MANUFACTURER THROUGH A COMPETENT PERSON BEFORE USING THE RAILS FOR MANUFACTURE. A PERSON POSSESSING A COMPETENCY CERTIFICATE ISSUED BY DIRECTOR GENERAL (M & C) RDSO SHALL BE DEEMED A COMPETENT PERSON.

15. NYLON CORD REINFORCED GRSP SHALL BE USED UNDER SLIDE CHAIRS, TIE PLATES AND SPECIAL BEARING PLATES AS SHOWN IN THE TABLE ALONG SIDE.

16. SINGLE COIL SPRING WASHERS TO DRAWING No T 10773 SHALL BE USED WITH ALL PLATE SCREWS TO DRAWING No. RDSOIT- 3913.

17. THE PART LIST OF THIS DRAWING DOES NOT INCLUDE FITTINGS FOR APPROACH SLEEPERS. THESE SHOULD BE INDENTED FOR SEPARATELY, IF REQUIRED.

18. HOLES FOR ADDITIONAL DISTANCE BLOCKS TO DRG. No. RDSOIT- 4359 & RDSOIT- 4360 IN LEAD RAILS WILL NORMALLY BE DRILLED AT SITE.

19. SINGLE COIL SPRING WASHERS TO DRG. No. T 10773 SHALL BE USED WITH ALL BOLTS OF 25 mm DIA.

20. THE HEADS OF BOLTS T 11524, T 11526 & T 11528 USED WITH BLOCKS SHALL BE LOCATED INSIDE THE TRACK GAUGE. THE WIDTH OF HEAD OF THESE BOLT SHALL BE REDUCED BY 4 mm BY MACHINING ON ONE SIDE TO ENABLE FITMENT.

21. P.S.C SLEEPERS USED IN THIS SWITCH ARE IDENTICAL TO THOSE USED IN 10125 mm CURVED SWITCH TO DRG. No. RDSOIT- 4219.

22. AT SLEEPER No. 15, ONE SIDE 45° BEVEL CUT HEAD BOLT T 11905 SHALL BE USED TO FASTEN SLIDE BLOCK WITH STOCK RAIL AS PER SECTION A-A.

23. THE STOCK RAILS ARE TO BE SUPPLIED BY THE MANUFACTURER. SLIDE BLOCKS SHALL BE BOLTED TO THE RESPECTIVE STOCK RAIL AND C.I. HEEL BLOCKS BOLTED IN PLACE AND THE TOE END OF THE TONGUE RAIL SHALL BE LASHED TO THE STOCK RAIL WITH STOUT WIRE.

24. SLIDE CHAIRS AND BOLTS ARE SAME FOR BOTH SIDES.

25. THOSE BOLTS WHICH ARE SKEW TO THE RAILS SHALL HAVE SPHERICAL WASHERS T 023 (M) & TAPERED PACKING PIECES RDSOIT- 2763 SHOWN ON THE DRAWING THUS: -

26. LATEST ALTERATION NUMBER SHALL BE CHECKED BEFORE PLACING ORDER.

27. ALL DIMENSIONS ARE IN MILLIMETRES.
27. PRE-CURVING OF TONGUE RAILS & STOCK RAILS FOR TURNOUTS OF CONTRARY FLEXURE & SIMILAR FLEXURE SHALL BE DONE AT MANUFACTURER'S PREMISES AS PER THE CURVATURE OF MAIN LINE AND CORRESPONDING VERSINE DETAILS GIVEN IN ANNEXURE - 46 & ANNEXURE - 47 OF IRPM.

28. M.S. TIE BAR TO DRG. No. RDSOIT- 9010 SHALL BE FIXED ON THE NON-POINT MACHINE END USING PLATE SCREW TO DRG. No. RDSOIT- 3913 AFTER 24 HOURS OF FIXING OF THE DOVEL.

29. IF DOVEL HOLES AT THE END OF SLEEPER No. 3 & 4 ARE NOT AVAILABLE FOR FIXING OF M.S. TIE BAR, ADDITIONAL HOLES OF 35 mm DIA. AND 165 mm DEPTH SHALL BE CAREFULLY DRILLED AS SHOWN IN DETAIL 'B' OF DRAWING No. RDSOIT- 6155 (ALT-12). POLYETHYLENE DOVEL TO DRG. No. RDSOIT- 3002 SHALL BE FIXED IN THE HOLE USING EPOXY RESIN OF TYPE L-100 CONFORMING TO IS: 12064-1990.

30. M.S. TIE BAR TO DRAWING No. RDSOIT- 9010/1 SHALL BE USED ON POINT MACHINE END AT SLEEPER No. 2AS, 1AS, 1, 2, 3, 4, 5 AS SHOWN ON LAYOUT DRAWING OF TURNOUT, RDSOIT- 6154.

31. M.S. TIE BAR TO DRAWING No. RDSOIT- 9010 SHALL BE USED ON NON-POINT MACHINE END AT SLEEPER No. 2AS, 1AS, 1, 2, 3, 4, 5 AS SHOWN ON LAYOUT DRAWINGS OF TURNOUT.

32. IN CASE OF REVELING OF JOINT AT SRJ, SLEEPER No. 1 CAN BE SHIFTED TOWARDS INSIDE SLIGHTLY SO THAT THE WELDED JOINT REMAINS IN FLOATING CONDITION & HOLE IN MS FLAT TIE BAR BE MADE ACCORDINGLY.

33. LEVER OF S.S.D. SHALL BE FIXED IN 28 DIA. HOLES DRILLED IN FOOT OF BOTH TONGUE RAILS AT J.O.H. ALONG WITH INSULATING BUSH.

34. THE CURVED TONGUE & STOCK RAILS SHALL BE GIVEN THE CORRECT BEND AS SHOWN IN DRG. No. RDSOIT- 6154 BY THE MANUFACTURE BEFORE DESPATCH FROM HIS WORKS WHILE INDENTING FOR THE TURNOUTS. THE RAILWAY SHALL CLEARLY INDICATE THE NUMBER OF L.H. & R.H. TURNOUT REQUIRED BY THEM AS THE CURVATURE OF TONGUE & STOCK RAILS GIVEN BY THE MANUFACTURER IS LIKELY TO GET DISTURBED DURING TRASIT TO THE SITE, THE SAME SHALL BE CHECKED & RECTIFIED BY THE S.E. (P.WAY) WHILE LAYING IN THE TRACK.

35. SLEEPER No. 21 AND ONWARD ARE LAID IN FANSHAPE.

36. A SPRING SETTING DEVICE (S.S.D.) IS TO BE PROVIDED NEAR JUNCTION OF RAIL HEADS (J.O.H).

37. OPERATION OF SWITCH IS TO BE CARRIED OUT ELECTRICALLY NEAR TOE OF SWITCH.

38. CLAMP POINT LOCK TO DRG. No. RDSOIS- 3454 SHALL BE USED BETWEEN SLEEPER No. 3 & 4 ALONG WITH 220 mm STROKE IRS POINT MACHINE.

39. WHEN THIS ASSEMBLY IS USED WITH 1 IN 12 CMS CROSSING TO DRG. No. RDSOIT- 4220, THE CHECK RAIL SHALL ALSO BE PROVIDED ALONG WITH COMPONENTS OF THIS SUB-ASSEMBLY.

NOTE

ITEM NO.	DESCRIPTION	QTY	UNIT
T-11528	BOLTS	25X310	2
RDSOIT- 9624	DISTANCE BLOCKS	1	1
RDSOIT- 9633	DISTANCE BLOCKS	12	1
RDSOIT- 9630	NYLON CORD REINFORCED GRSP	12	84
RDSOIT- 9818	ELASTIC RAIL CLIP M.K.V.	76	84
RDSOIT- 3740	METAL LINER	1	1
RDSOIT- 9619/1	M.S. FLAT TIE BAR	1	1
RDSOIT- 9010	M.S. FLAT TIE BAR	1	1
TO DETAILCOMPONENT OF S.S.D.			
RDSOIT- 6017/28	WEDGE	34	2
RDSOIT- 6305/A	WEDGE	34	2
RDSOIT- 9807	NYLON CORD REINFORCED GRSP	42	2
RDSOIT- 6805	NYLON CORD REINFORCED GRSP	42	2
RDSOIT- 9554	NYLON CORD REINFORCED GRSP	4	6
RDSOIT- 9889	NYLON CORD REINFORCED GRSP	8	6
RDSOIT- 9895	NYLON CORD REINFORCED GRSP	8	6
RDSOIT- 9894	NYLON CORD REINFORCED GRSP	2	2
RDSOIT- 9893	NYLON CORD REINFORCED GRSP	36	4
RDSOIT- 9806	NYLON CORD REINFORCED GRSP	36	4
RDSOIT- 6310	LEAF SPRING	36	4
RDSOIT- 4616	CHECK RAILS	1	2
RDSOIT- 6216	SPRING SETTING DEVICE	1	8
RDSOIT- 2881	PACKING PIECES	8	1
RDSOIT- 2763	PACKING PIECES (TAPERED)	8	1
RDSOIT- 9631	M.S. PLATES	239	1
RDSOIT- 3913	PLATE SCREWS	2	216
T-11533	BOLTS	25X330	2
T-11531	BOLTS	25X300	2
T-11528	BOLTS	25X330	2
T-11524	BOLTS	25X250	4
T-11505	BOLTS	25X100	12
RDSOIT- 9817	CAST STEEL SPECIAL BEARING PLATES	2	2
RDSOIT- 6191	CAST STEEL SPECIAL BEARING PLATES	ONE EACH	8
RDSOIT- 3706	INSULATING LINER	ONE SET	4
RDSOIT- 9632	INSULATED TIE PLATES FOR SLEEPER NO. 13	ONE SET	4
RDSOIT- 9632/1	SPHERICAL WASHERS	34	4
RDSOIT- 9616	SLIDE CHAIRS	ONE SET	4
RDSOIT- 9653	CAST STEEL/MILD STEEL EXTENDED TIE PLATE (INSULATED) (ON SL. No. 03)	ONE SET	4
RDSOIT- 4180	SLIDE BLOCKS	ONE EACH	2
RDSOIT- 6191	SLIDE BLOCKS	ONE EACH	2
RDSOIT- 4359	DISTANCE BLOCKS	2	1
RDSOIT- 2762	DISTANCE BLOCKS	2	1
RDSOIT- 2761	DISTANCE BLOCKS	1	1
RDSOIT- 2774	HEEL BLOCKS	ONE EACH	2
RDSOIT- 2775	TONGUE RAIL LEFT	1	1
RDSOIT- 6155/1	TONGUE RAIL RIGHT	1	1
RDSOIT- 6155/1	STOCK RAIL LEFT	1	1
RDSOIT- 6155/1	STOCK RAIL RIGHT	1	1
PART DESCRIPTION No. OFF			
THIS DRAWING IS THE PROPERTY OF RESEARCH DESIGNS AND STANDARDS ORGANISATION (MINISTRY OF RAILWAYS) LUCKNOW-226011, INDIA AND SHALL NOT BE USED, COPIED OR REPRODUCED IN PART OR WHOLE, WITHOUT PRIOR CONSENT IN WRITING.			
R.	D.	S.	O.
10125 mm CURVED SWITCH WITH ZU-1-60/60E1A1 THICK-WEB TONGUE RAILS FOR 1 IN 12 TURNOUT B.G. (1673 mm) FOR 60 kg (UIC)/60E1 ON P.S.C. SLEEPERS		01-10-2024	22-05-2024
STAMP: _____	ADVANCE: _____	(T)	