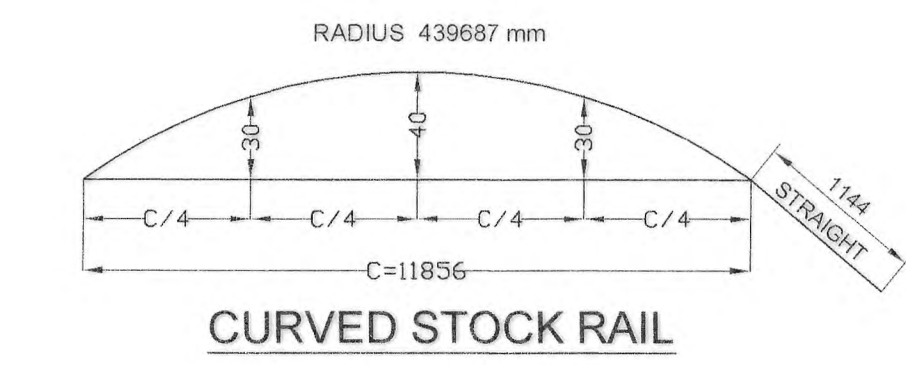
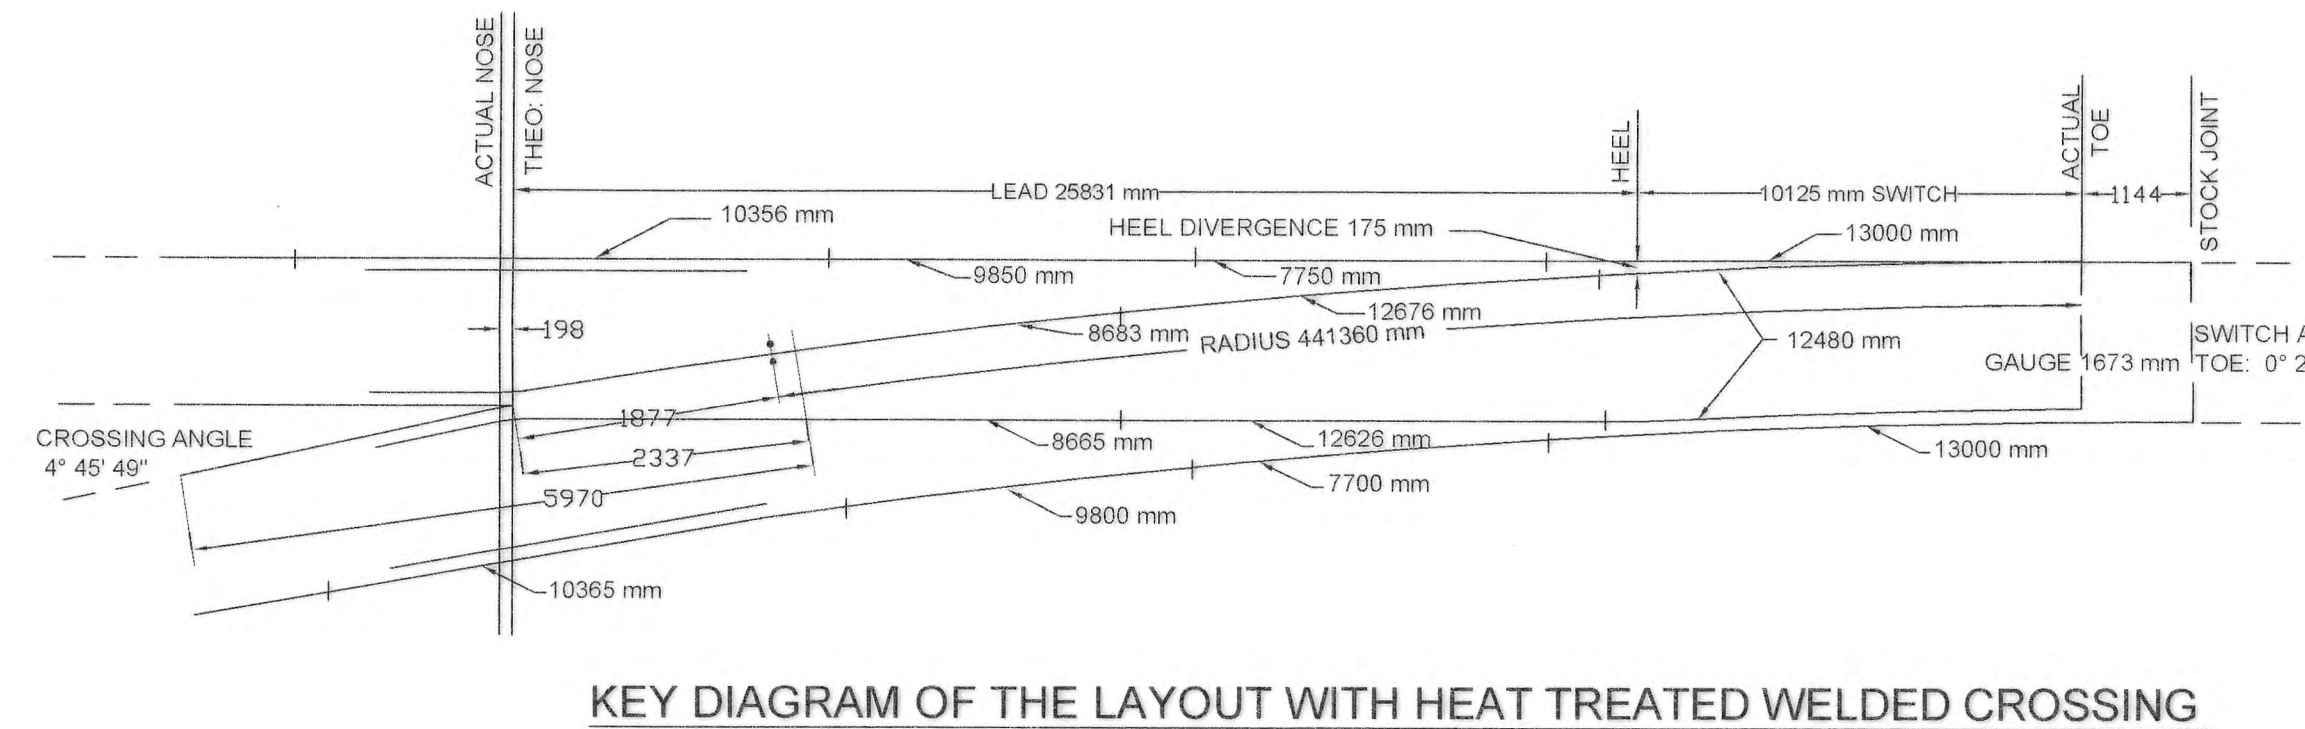
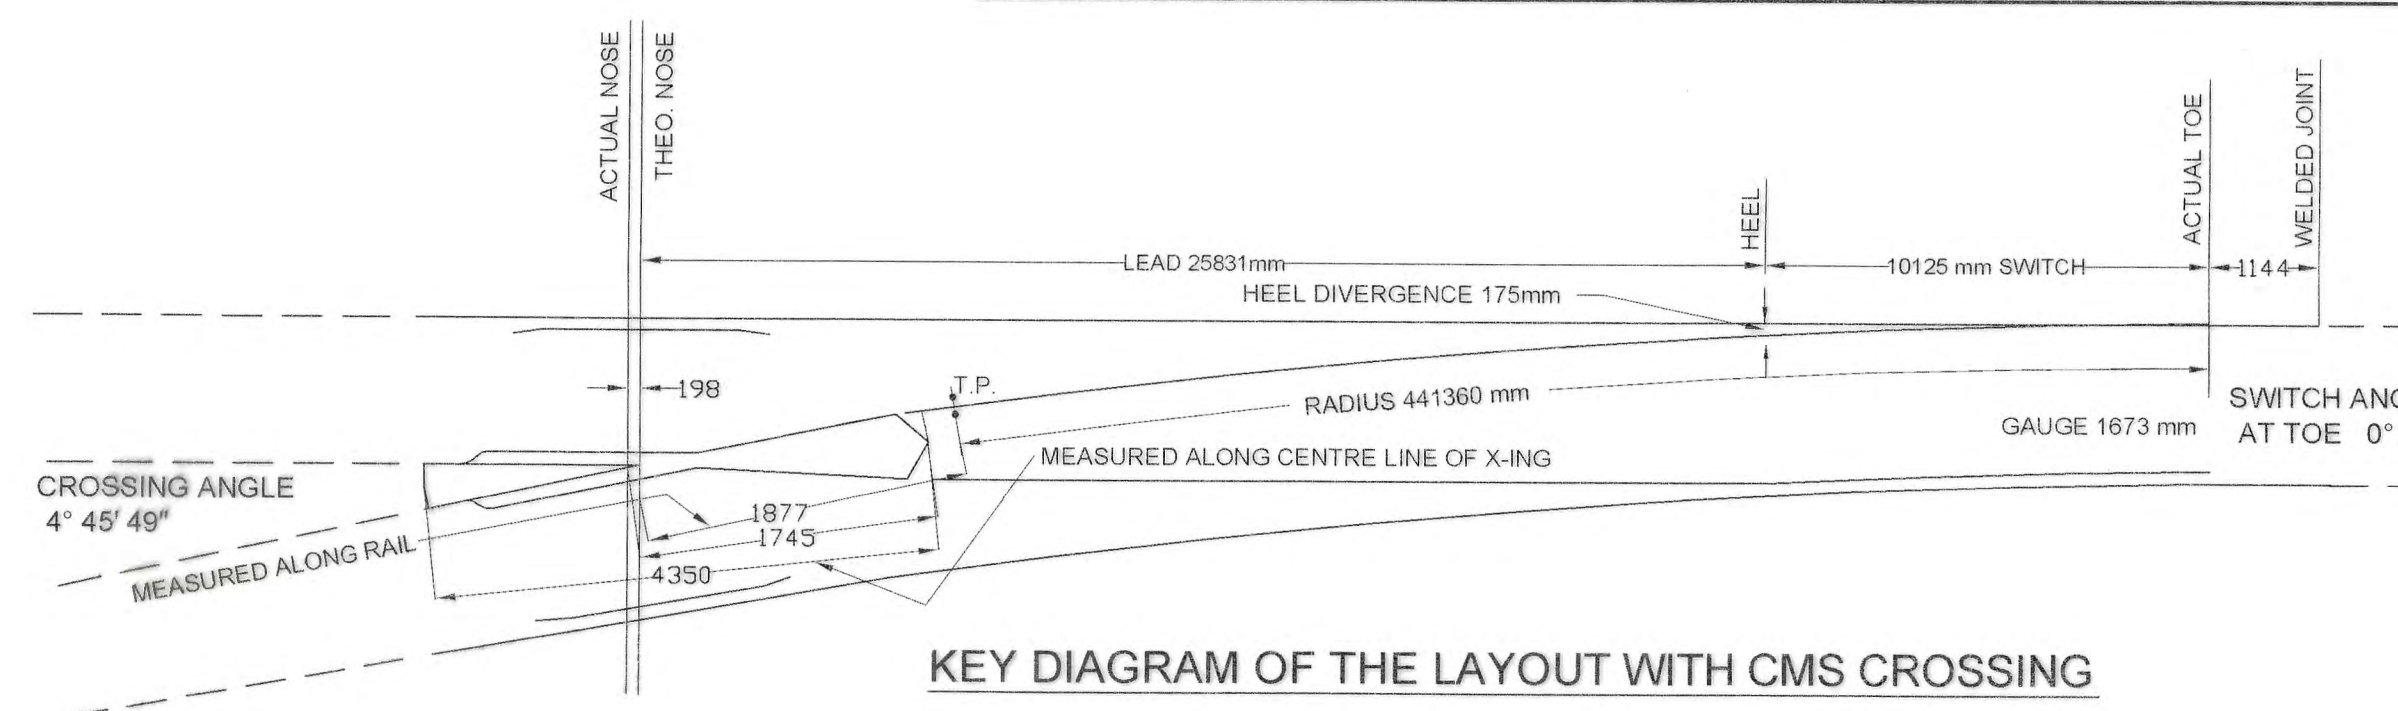
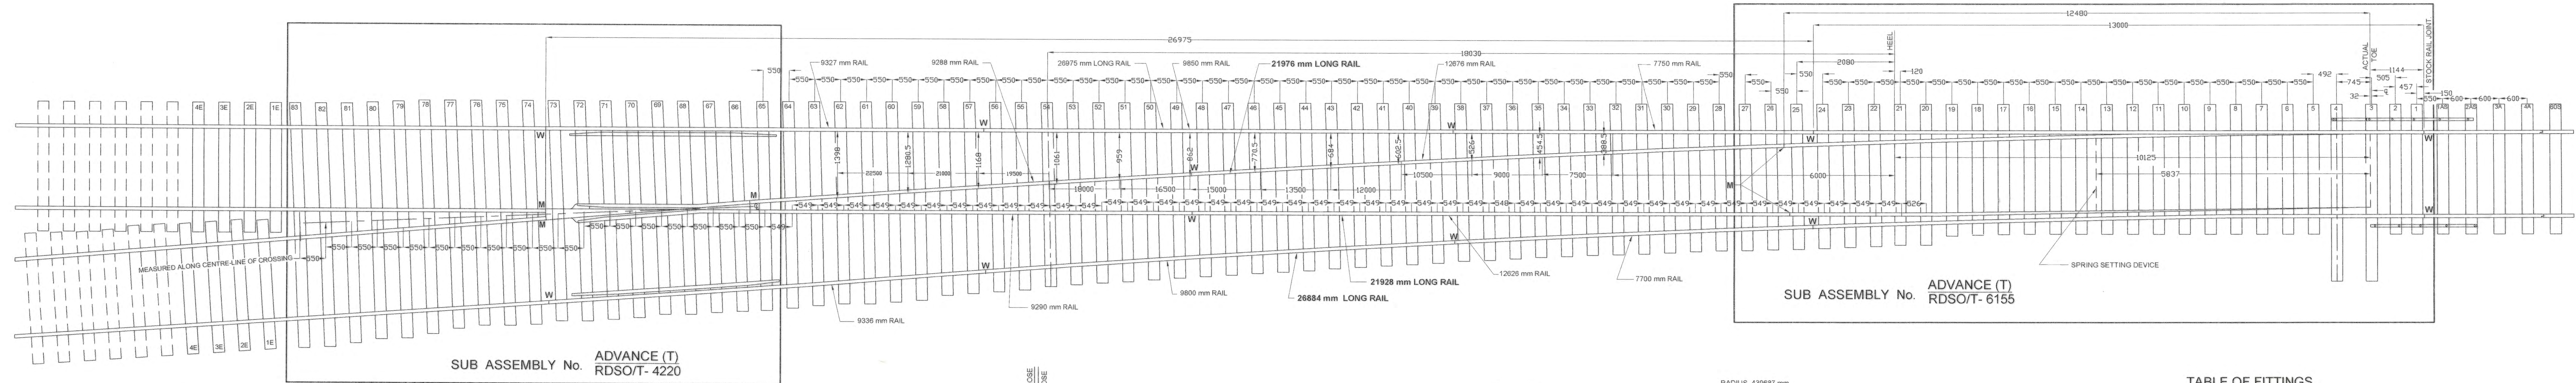


CHECKING OF CURVES FOR TONGUE AND STOCK RAILS AT SITE

TABLE OF FITTINGS

SLEEPER S. No.	NYLON CORD REINFORCED GRSP			INSULATING LINER RDSO/T- 3706	ERC MK-V RDSO/T- 5919	M.S. PLATE RDSO/T- 3902	PLATE SCREW RDSO/T- 3912
	RDSO/T- 8889	RDSO/T- 8886	RDSO/T- 8890				
APPROACH PORTION:							
60 S	2	---	---	4	4	1	6
60-4A	2	---	---	4	4	---	---
60-3A	2	---	---	4	4	---	---
60-2AS	2	---	---	4	4	1	6
60-1AS	2	---	---	4	4	1	6
SWITCH PORTION: PLEASE REFER DRG. No. RDSO/T- 6155							
LEAD PORTION:							
28 TO 63	---	144	---	288	288	---	---
64	---	2	1	7	7	---	---
CROSSING PORTION: PLEASE REFER DRG. No. RDSO/T- 4220							
EXIT PORTION:							
1 E X 2	4	---	---	8	8	---	---
2 E X 2	4	---	---	8	8	---	---
3 E X 2	4	---	---	8	8	---	---
4 E X 2	4	---	---	8	8	---	---

NOTE: E INDICATES - EXIT SLEEPERS.
60 INDICATES - 60 kg RAIL SECTION.
S INDICATES - SLEEPERS WITH SIGNAL FITTING.
A INDICATES - APPROACH SLEEPERS.

TABLE OF SLEEPERS

SLEEPER S. No.	DRAWING No.	LENGTH	SLEEPER S. No.	DRAWING No.	LENGTH
60S	RDSO/T- 4786	2750	43	RDSO/T- 4554	3330
60-4A	RDSO/T- 4790	2750	44	RDSO/T- 4555	3360
60-3A	RDSO/T- 4789	2750	45	RDSO/T- 4556	3390
60-2AS	RDSO/T- 4788	2750	46	RDSO/T- 4557	3420
60-1AS	RDSO/T- 4787	2750	47	RDSO/T- 4558	3460
1	RDSO/T- 4512	2750	48	RDSO/T- 4559	3490
2	RDSO/T- 4512	2750	49	RDSO/T- 4560	3520
3	RDSO/T- 4514	3750	50	RDSO/T- 4561	3560
4	RDSO/T- 4515	3750	51	RDSO/T- 4562	3600
5	RDSO/T- 4516	2750	52	RDSO/T- 4563	3630
6	RDSO/T- 4517	2750	53	RDSO/T- 4564	3670
7	RDSO/T- 4518	2750	54	RDSO/T- 4565	3710
8	RDSO/T- 4519	2750	55	RDSO/T- 4566	3750
9	RDSO/T- 4520	2750	56	RDSO/T- 4567	3790
10	RDSO/T- 4521	2750	57	RDSO/T- 4568	3830
11	RDSO/T- 4522	2750	58	RDSO/T- 4569	3870
12	RDSO/T- 4523	2750	59	RDSO/T- 4570	3910
13	RDSO/T- 4524	2750	60	RDSO/T- 4571	3950
14	RDSO/T- 4525	2750	61	RDSO/T- 4572	3990
15	RDSO/T- 4526	2750	62	RDSO/T- 4573	4040
16	RDSO/T- 4527	2750	63	RDSO/T- 4574	4080
17	RDSO/T- 4528	2760	64	RDSO/T- 4575	4120
18	RDSO/T- 4529	2770	65	RDSO/T- 4576	4170
19	RDSO/T- 4530	2790	66	RDSO/T- 4577	4220
20	RDSO/T- 4531	2800	67	RDSO/T- 4578	4260
21	RDSO/T- 4532	2820	68	RDSO/T- 4579	4310
22	RDSO/T- 4533	2830	69	RDSO/T- 4580	4360
23	RDSO/T- 4534	2850	70	RDSO/T- 4581	4400
24	RDSO/T- 4535	2870	71	RDSO/T- 4582	4440
25	RDSO/T- 4536	2890	72	RDSO/T- 4583	4490
26	RDSO/T- 4537	2900	73	RDSO/T- 4584	4540
27	RDSO/T- 4538	2920	74	RDSO/T- 4585	4580
28	RDSO/T- 4539	2940	75	RDSO/T- 4586	4630
29	RDSO/T- 4540	2960	76	RDSO/T- 4587	4680
30	RDSO/T- 4541	2990	77	RDSO/T- 4588	4720
31	RDSO/T- 4542	3010	78	RDSO/T- 4589	4770
32	RDSO/T- 4543	3030	79	RDSO/T- 4590	4810
33	RDSO/T- 4544	3050	80	RDSO/T- 4591	4850
34	RDSO/T- 4545	3080	81	RDSO/T- 4592	4890
35	RDSO/T- 4546	3100	82	RDSO/T- 4593	4930
36	RDSO/T- 4547	3130	83	RDSO/T- 4594	4970
37	RDSO/T- 4548	3160	1E	RDSO/T- 5471	2550
38	RDSO/T- 4549	3180	2E	RDSO/T- 5472	2550
39	RDSO/T- 4550	3210	3E	RDSO/T- 5473	2550
40	RDSO/T- 4551	3240	4E	RDSO/T- 5474	2550
41	RDSO/T- 4552	3270			
42	RDSO/T- 4553	3300			

NOTE

- THE SAME SET OF SLEEPERS FROM No. 1 TO 83 AND APPROACH SLEEPERS CAN BE USED IN RH TURNOUT ALSO.
- SLEEPER No. 1 TO 20 ARE PERPENDICULAR TO THE MAIN LINE AND SLEEPER No. 65 TO 83 ARE PERPENDICULAR TO THE CENTRE LINE OF CROSSING.
- SLEEPER No. 21 TO 84 ARE LAID IN 'FAN' SHAPE' i.e. THEIR SPACINGS ARE DIFFERENT AT RH AND LH GAUGE FACES OF STRAIGHT TRACK.
- GIVEN SLEEPER SPACINGS SHALL BE MEASURED AT THE GAUGE FACES OF RIGHT AND LEFT RAILS OF MAIN LINE TRACK UNLESS OTHERWISE SPECIFIED.
- ALL JOINTS IN THE TURNOUT SHALL BE WELDED JOINTS EXCEPT FOR THE TONGUE RAIL & CROSSING JOINTS WHICH SHALL BE MACHINED JOINTS. THE WELDED JOINTS SHOULD PREFERABLY BE FLASH BUTT WELDED. CARE SHOULD BE TAKEN TO ENSURE THAT THE WELDED JOINTS REMAIN SUSPENDED BETWEEN THE SLEEPERS. CUT RAILS OF SUITABLE LENGTH SHOULD BE USED FOR THIS PURPOSE.
- THE JOINTS MARKED 'M' SHALL BE MACHINED JOINTS TO DRAWING No. RDSO/T- 2594. THE END FACES OF THE RAILS IN THESE JOINTS SHALL BE MACHINED TRUE AND SQUARE. THE RAILS SHALL HAVE TWO 28.5 mm DIA. HOLES FOR FISH BOLTS LOCATED AT 83 mm AND 249 mm FROM THE ENDS.
- THE CHANGE OF RAILS FROM THE VERTICAL POSITION IN THE CANTED POSITION OUTSIDE SHALL BE DONE AHEAD OF THE STOCK JOINT AND BEHIND THE HEEL OF CROSSING BY USING APPROACH AND EXIT SLEEPERS WITH UNIFORMLY VARYING CANT.
- OFFSETS ARE GIVEN FROM GAUGE FACE TO GAUGE FACE.
- THE APPROACH SLEEPERS SHOULD BE LAID PERPENDICULAR TO THE TRACK TO WHICH THEY CATER FOR.
- LATEST ALTERATION NUMBER SHALL BE CHECKED BEFORE PLACING ORDERS.
- ALL DIMENSIONS ARE IN MILLIMETRES.
- Holes for fixing clamp point lock brackets in stock and tongue rails both shall be done at site as per guidelines issued by RDSO.
- Pin brazing connection shall be given to connect bond wires from one rail to other instead of drilling holes to avoid weakening of rails.
- Operation of switch shall be carried out electrically near toe of switch. A spring setting device shall be provided near J.O.H.
- Length of M.S. flat tie bar may be kept upto sleeper No. 2AS as per site requirements.
- The curved tongue and stock rails shall be given the correct bend as shown in this drawing by the manufacturer before despatch from the works while indenting for the turnouts. The railways shall clearly indicate the number of L.H. & R.H. turnouts required by them. As the curvature of tongue and stock rails given by the manufacturer is likely to get disturbed during transit to site, the same shall be checked and rectified by S.E. (P. Way) while laying in the track.
- Single coil spring washer to DRG. No. T 10773 shall be used with all plate screws to DRG. No. RdsO/T- 3912.
- The head, web and foot of each rail shall be ultrasonically tested by the manufacturer through a competent person before using the rails for manufacture. A person possessing a competency certificate issued by Director General (M&C) RDSO shall be deemed a competent person.
- Holes of 28.5 mm dia. at the ends of rails used for manufacture of switches & crossings shall be chamfered by the manufacturer. For this purpose, chamfering tools to DRG. No. RDSO/T- 5210 to RDSO/T- 5212 shall be used.
- The part list of this drawing shows only the fittings required for the area outside sub-assemblies RDSO/T- 6155 & RDSO/T- 4220 enclosed by rectangles. For fittings inside these rectangles see part lists of drawings RDSO/T- 6155 & RDSO/T- 4220.

IRS: T 10.

NOT TO SCALE

06.

REVISED & REDRAWN

- NOTE No. 20 ADDED
- ELASTIC RAIL CLIPS MK-II ARE REPLACED WITH ELASTIC RAIL CLIPS MK-V
- BEND PROVIDED IN M.S. FLAT TIE BAR TO DRG. No. RDSO/T- 9010

12-10-2023

STANDARD
CARRIED
REVISED

ADVANCE
28-11-2002
(T)

SPECIFICATION

SCALE

ALT:

DESCRIPTION

DATE

RDSO/T- 6154